

_rus

александр —
мирошин

2018 —
2024

часть — архитектурное портфолио

2025




Образование

Работа

Приоритеты:



Рабочий процесс:

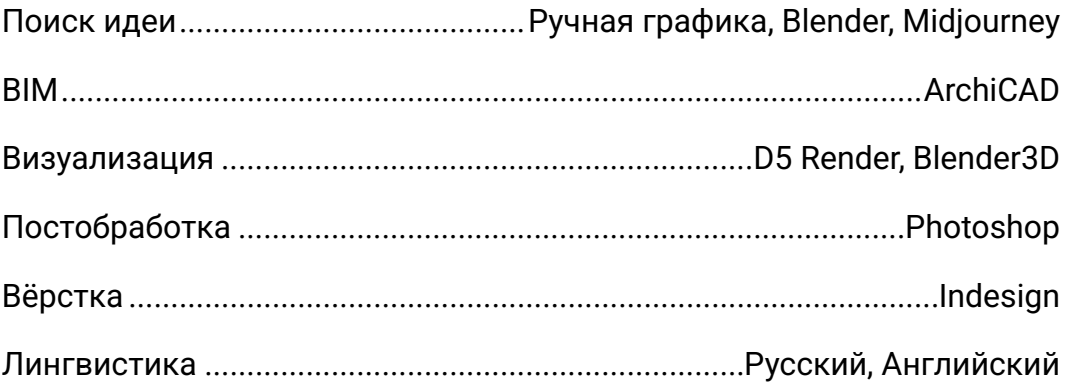

При необходимости также:

Revit, SketchUp, AutoCAD, Figma, Stable Diffusion

Контакты:

- 📍 Нижний Новгород, Россия
- ☎ +7 (986) 156-78-65 (WhatsApp/Telegram)
- ✉ miroshin.architect@gmail.com
- 📧 a_miroshin

2025

2024

2020

2018

2015

ННДК Л ПРОЕКТ - архитектор
ООО "Перспектива" - архитектор стадии РД

"HEADSGROUP" - Архитектор-концептуалист

"KNGK-GROUP" - Архитектор-концептуалист

Фриланс - архитектор-концептуалист

"Builart" - дизайнер интерьера

ЗАО "Межрегиональный Институт Градостроительства" - архитектор-концептуалист

Архитектурная Мастерская ННГАСУ - стажировка

Фестиваль "Арххакатон" - Куратор образовательной программы

Нижегородский Государственный Архитектурно-Строительный Университет (ННГАСУ)- Градостроительное проектирование - Бакалавриат

Все дети - художники.
Проблема в том, чтобы
остаться художником, когда
ты вырос.

содержание///

школа_в_ольгино	5
/	
/	
застывший_флот	15
/	
/	
жк_королев	27
/	
/	
эффект_бабочки	39
/	
/	
цепь_советов.....	51
/	
/	
/	
/	
/	
[[проект_вашей_компании(?)]] ...	61

школа_в_ольгино///



Категория: Студенческий проект
Год: 2018
Типология: Общеобразовательная школа
Вместимость: 1000 школьников
Пл. застройки: 3000 кв.м.

Инструменты
ArchiCAD, SketchUp, V-Ray

Ситуация


Концепция данного архитектурного объекта базируется на формообразовании с использованием простейшей геометрической фигуры - квадрата.

Основная цель данной композиции - создать хорошо освещенные как кабинеты, так и коридоры. А внутренний двор обеспечит возможность прогулки детям младших классов под присмотром руководителя, находящегося внутри здания.

Проект выполняется в монолитном ж/б каркасе. 1 и 2 этажи облицованы старым керамическим кирпичом, третий - оштукатурен.


Экспликация ситуации:

- 1. Участок школы
- 2. Стадион
- 3. Озеро
- 4. Приходской комплект
- 5. Общественно-деловая зона

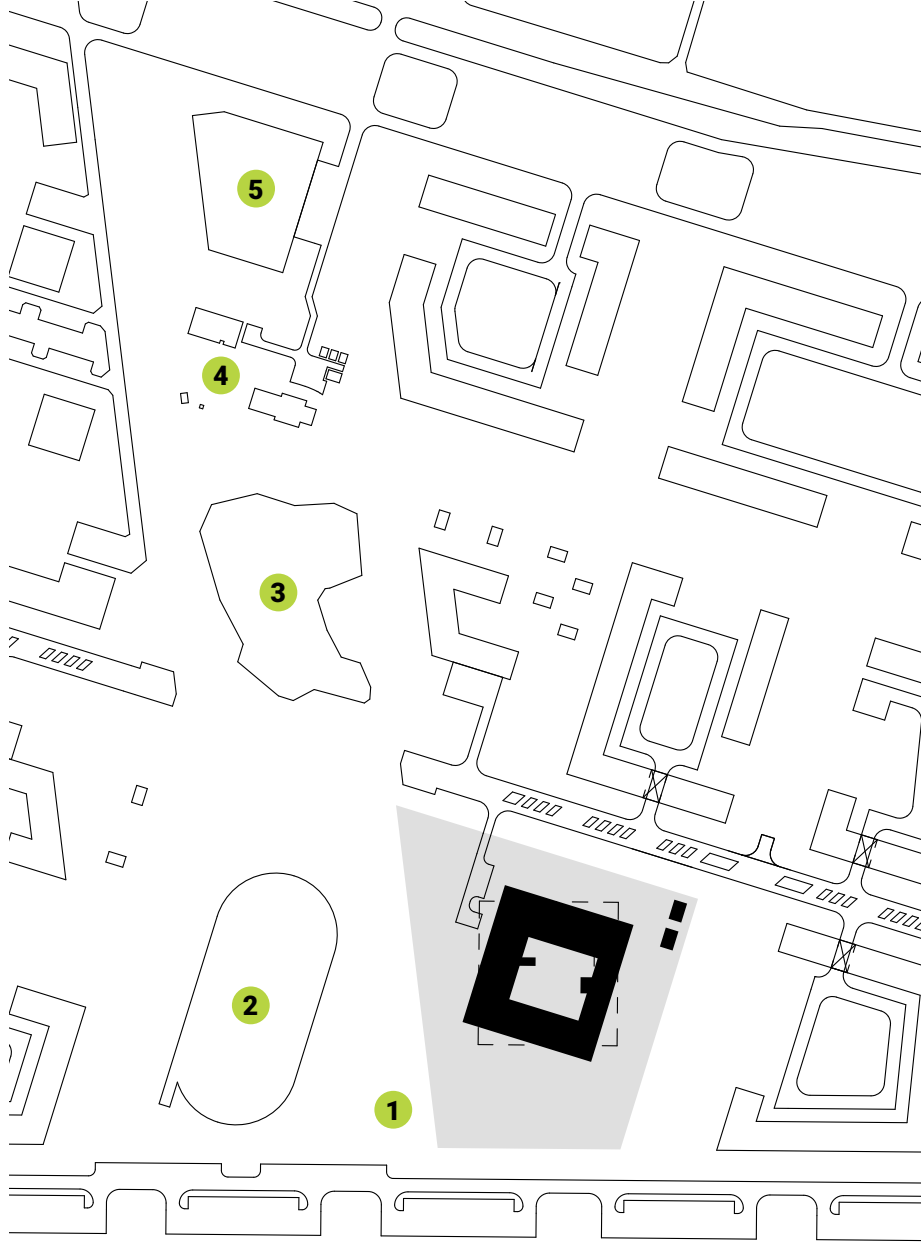





обыкновенная
прямоугольная коробка

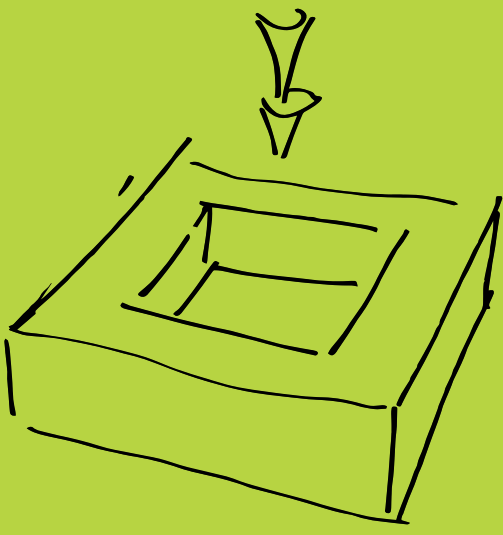

Создаем внутренний двор

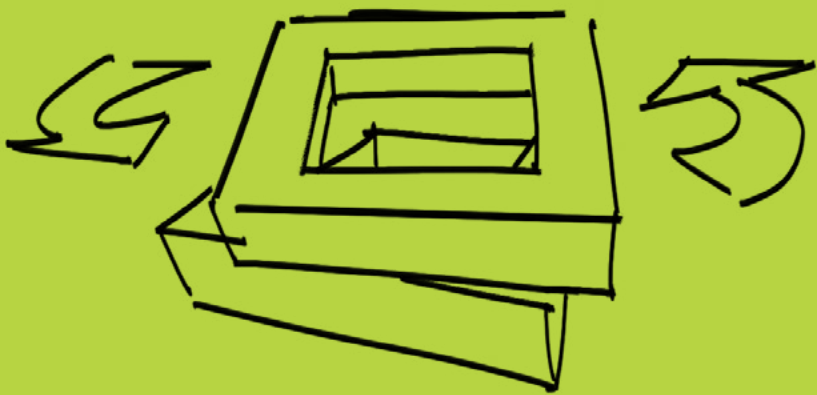



Нарезаем этажи, обращаем 3-й
фасадом на сновное пешеходное
движение

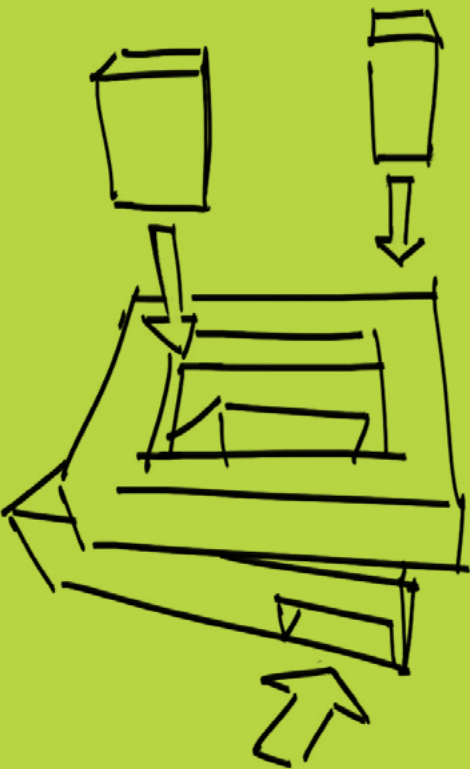

Врезка объемов
лестничных узлов во
внутренний двор

Концепция


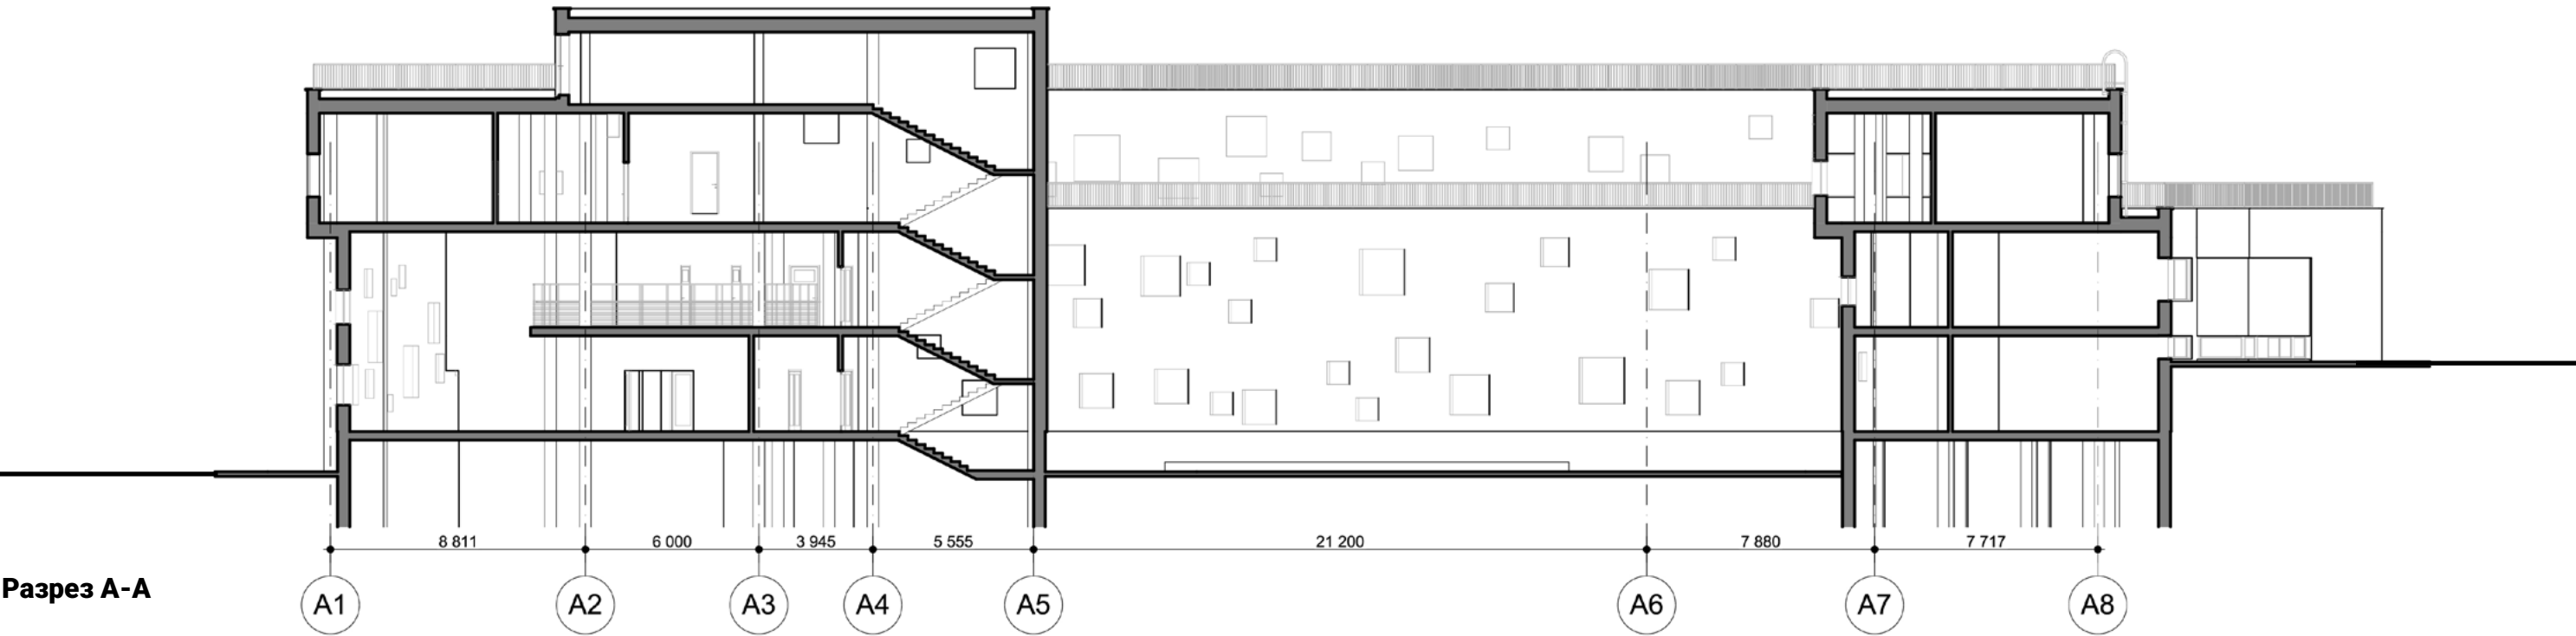


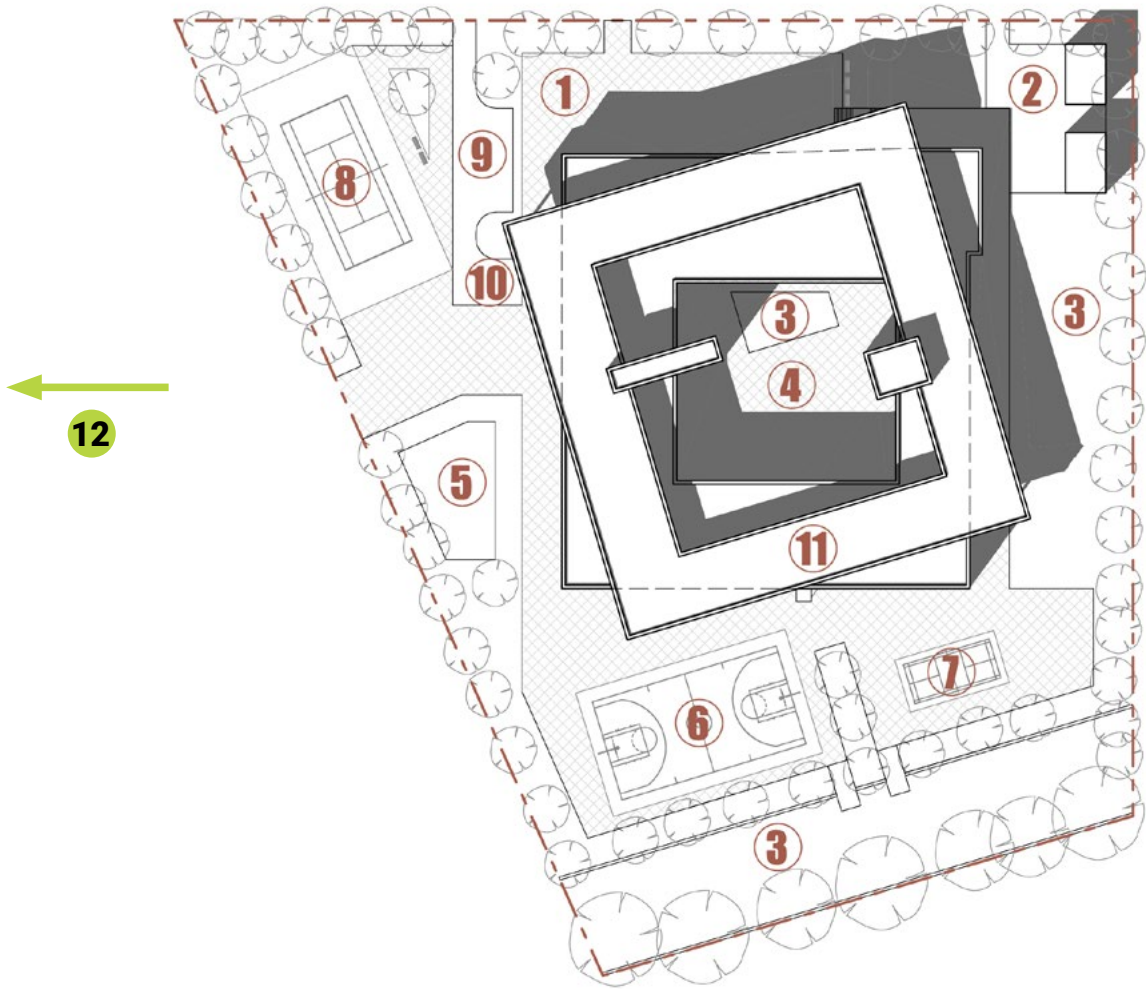

Генеральный план


Экспликация помещений:

- | | | |
|----------------------------|------------------------------------|-------------------------------------|
| 1. Входная группа | 6. Баскетбольная площадка | 10. Зона разгрузки |
| 2. Хозяйственная зона | 7. Площадка для бадминтона | 11. Зона принятия солнечных ванн |
| 3. Зона отдыха с цветником | 8. Теннисная площадка | 12. Стадион (не показан на чертеже) |
| 4. Внутренний двор | 9. Стоянка личных авто сотрудников | |
| 5. Фонтан | | |

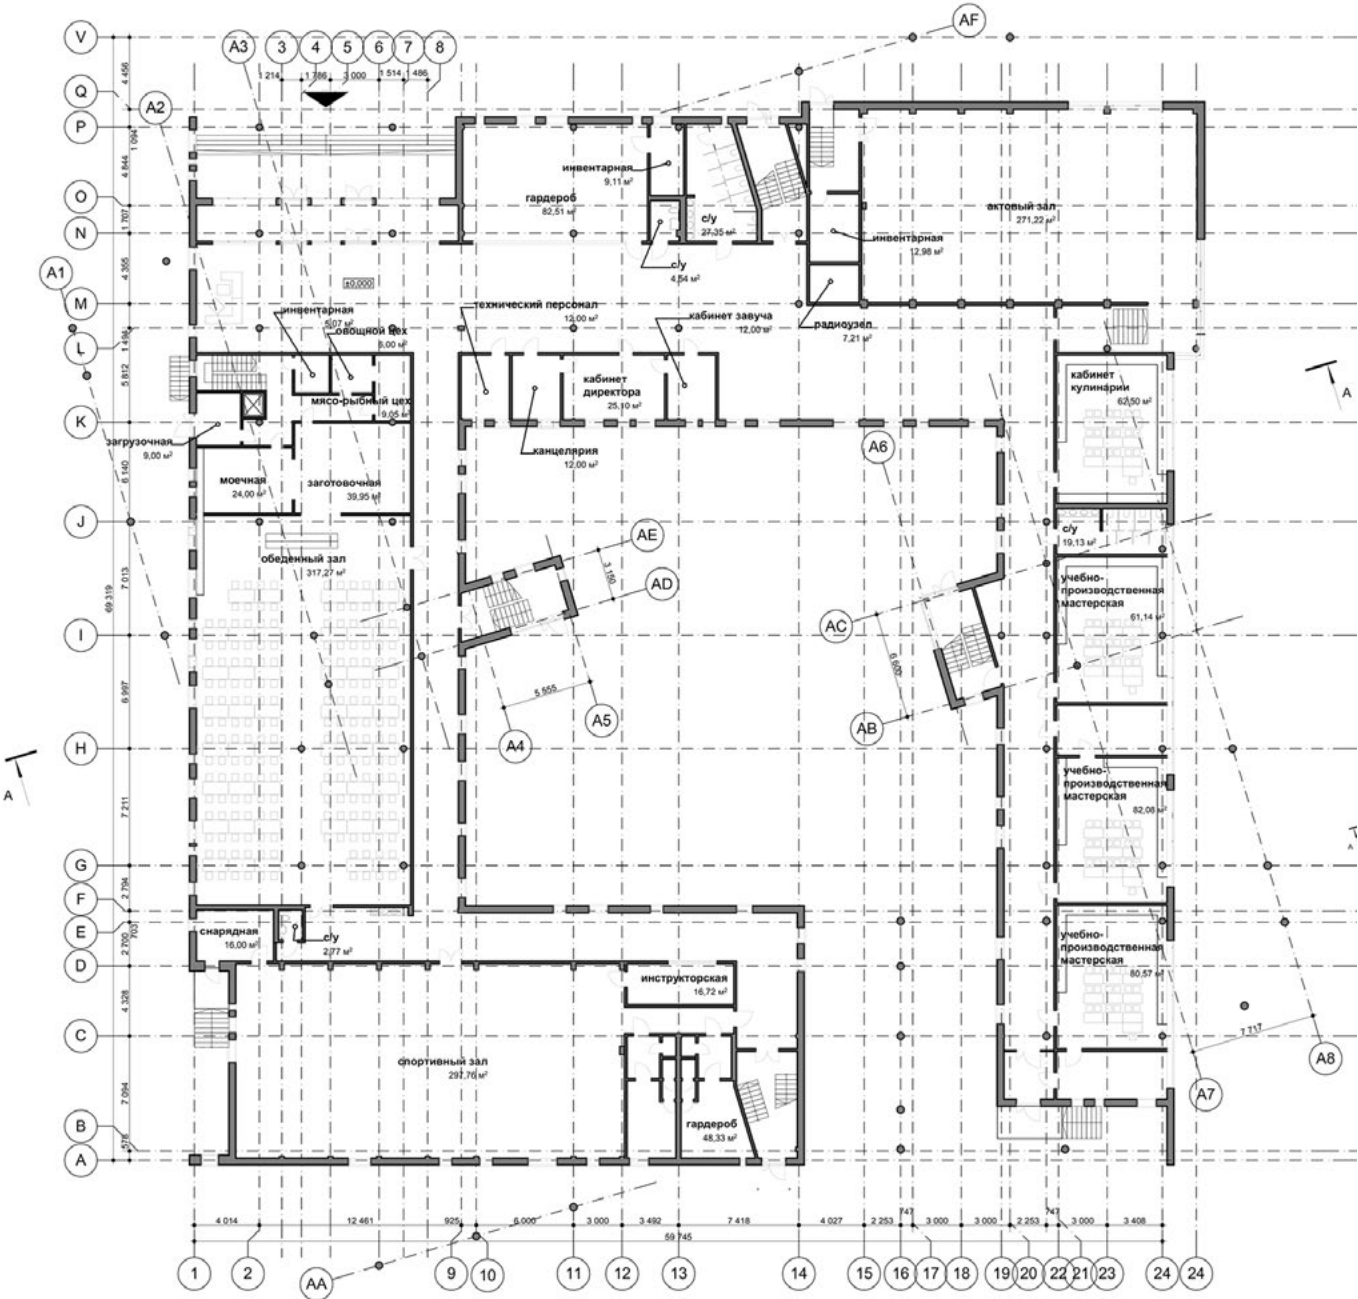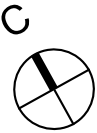


План 1-го этажа

Экспликация помещений:

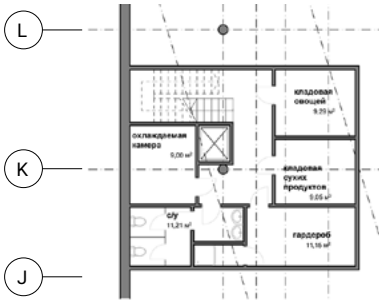


План подвального этажа

1. Фойе
2. Коридор
3. Гардероб
4. Инвентарная
5. С/У
6. Л/К
7. Радиоузел
8. Входное помещение
9. Кабинет тех. Персонала
10. Канцелярия
11. Кабинет директора
12. Кабинет завуча
13. Актовый зал

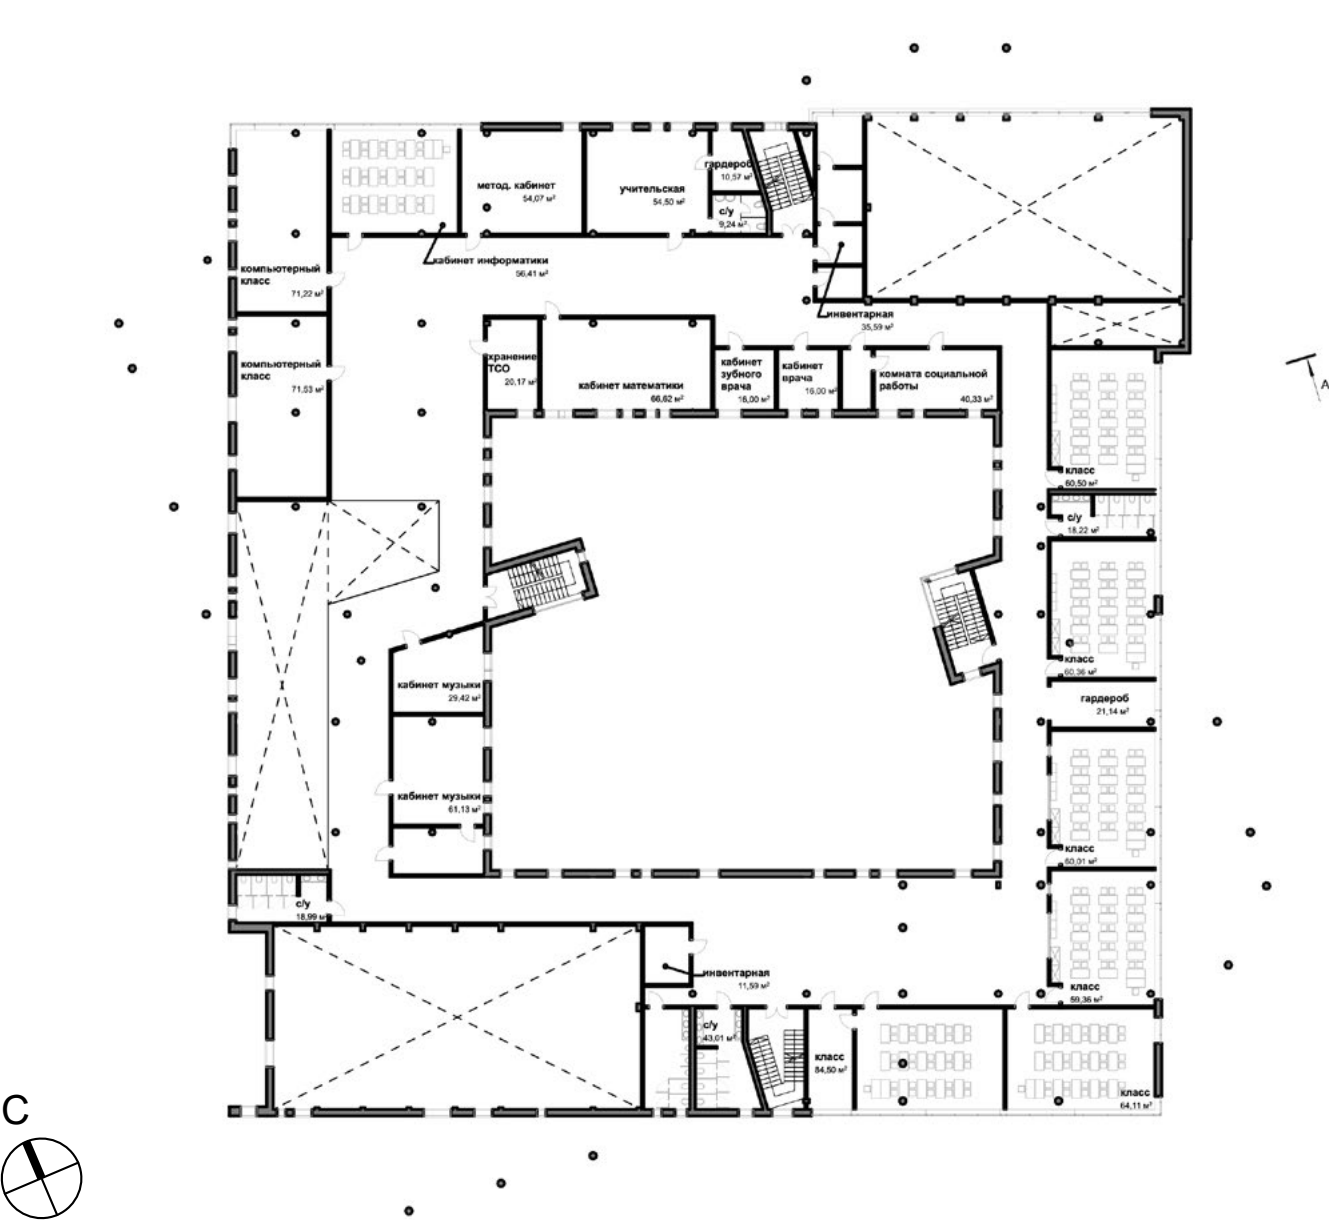


План 2-го этажа

- | | | |
|---------------------------------|------------------------------|-------------------------|
| 14. Кабинет кулинарии | 27. Обеденный зал` | 40. Л/К |
| 15. С/У | 28. Заготовочная | 41. Инвентарная |
| 16. Л/К | 29. Моечная | 42. Балкон |
| 17. Учебно-производ. мастерская | 30. Мясо-рыбный цех | 43. Каб. Зубного врача |
| 18. Учебно-производ. мастерская | 31. Инвентарная | 44. Каб. врача |
| 19. Учебно-производ. мастерская | 32. Овощной цех | 45. Комната соц. работы |
| 20. Входное помещение | 33. Загрузочная | 46. Класс |
| 21. Л/К | 34. Л/Л/У | 47. С/У |
| 22. Гардероб | 35. Кладовая овощей | 48. Класс |
| 23. Инструкторская | 36. Кладовая сухих продуктов | 49. Гардероб |
| 24. Спортивный зал | 37. Охлаждаемая камера | 50. Класс |
| 25. С/У | 38. С/У | 51. Класс |
| 26. Снарядная | 39. Гардероб | 52. Класс |

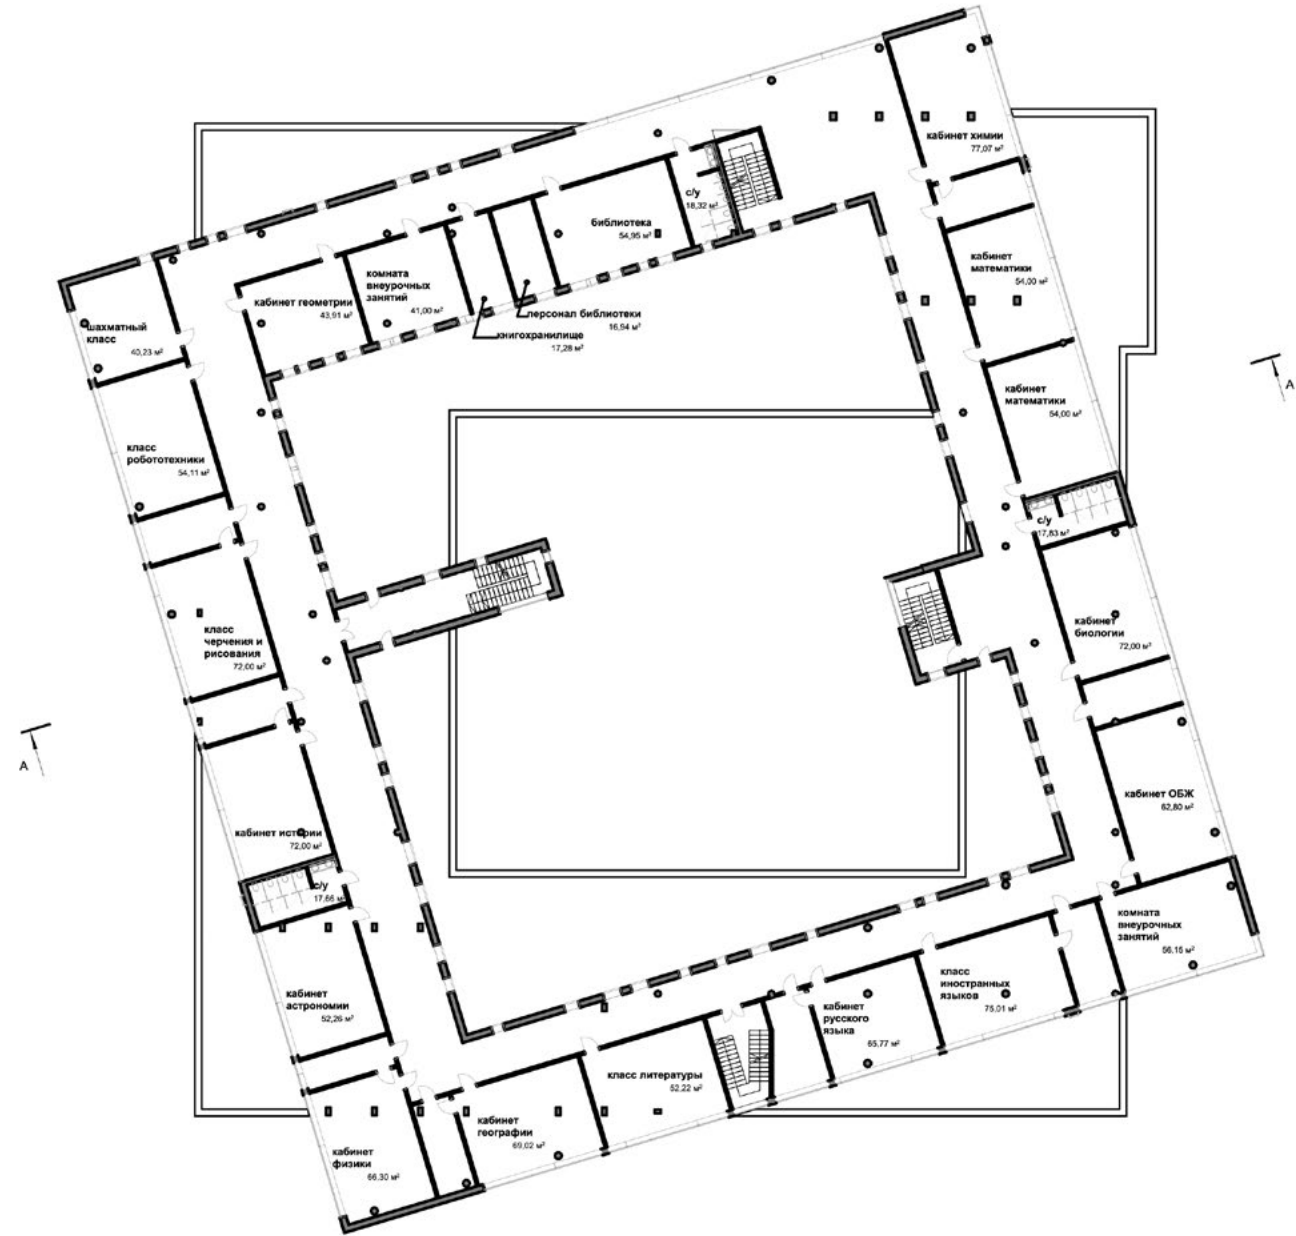


План 3-го этажа

- | | | |
|-------------------------|------------------------------|--------------------------------|
| 53. Класс | 66. Комната хранения ТСО | 79. Каб. физики |
| 54. С/У | 67. Кабинет математики | 80. Каб. астрономии |
| 55. Инвентарная | 68. Каб. химии | 81. С/У |
| 56. С/У | 69. Каб. математики | 82. Каб. истории |
| 57. Кабинет музыки | 70. Каб. математики | 83. Класс черчения и рисования |
| 58. Кабинет музыки | 71. С/У | 84. Класс робототехники |
| 59. Компьютерный класс | 72. Каб. биологии | 85. Шахматный класс |
| 60. Компьютерный класс | 73. Каб. ОБЖ | 86. Каб. геометрии |
| 61. Кабинет информатики | 74. Ком. внеурочных занятий | 87. Ком. внеурочных занятий |
| 62. метод. кабинет | 75. Класс иностранных языков | 88. Книгохранилище |
| 63. Учительская | 76. Каб. русского языка | 89. Ком. персонала библиотеки |
| 64. Гардероб | 77. Класс литературы | 90. Библиотека |
| 65. С/У | 78. Каб. географии | 91. С/У |

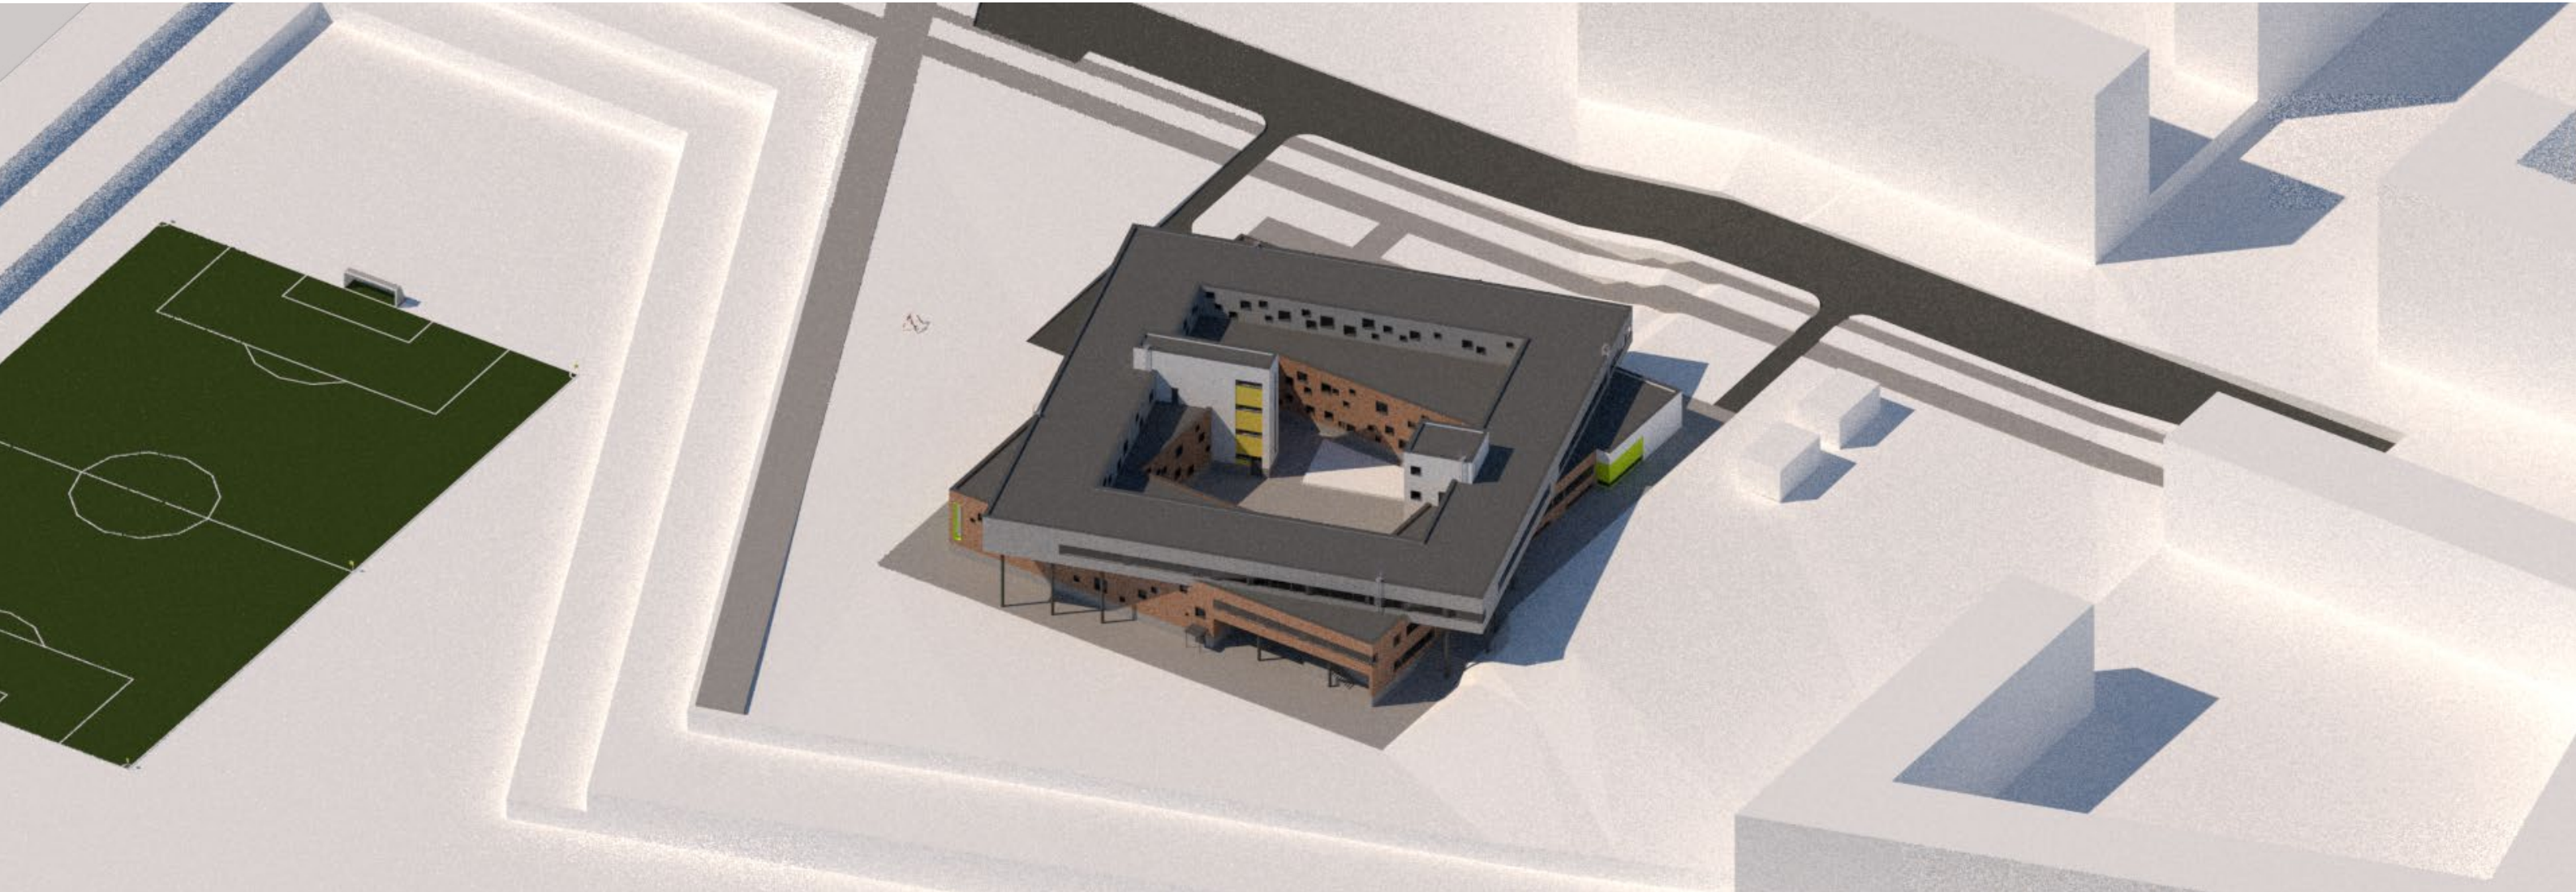

Аксометрия

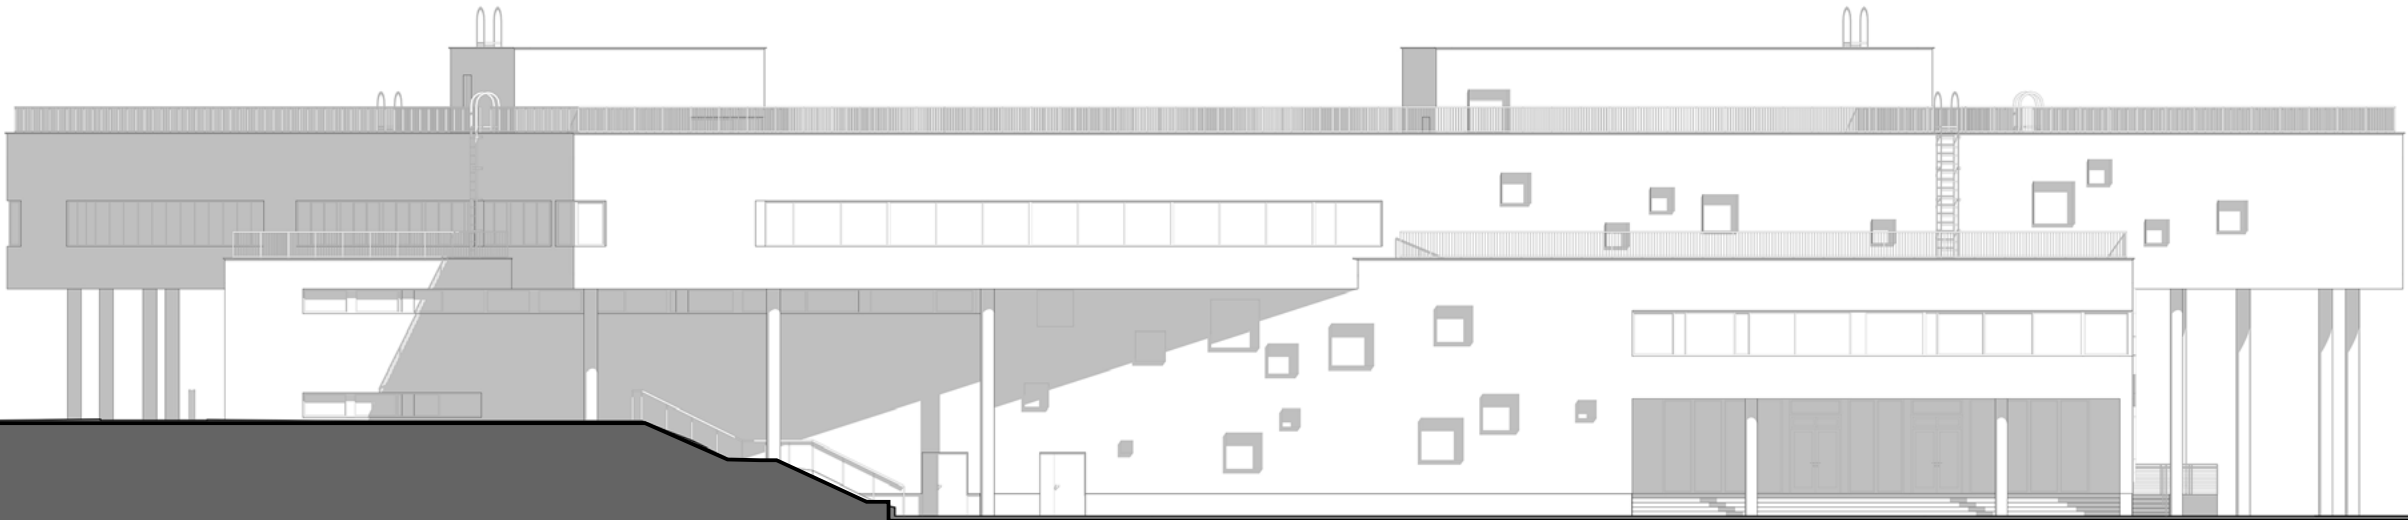

Главный фасад

застывший_ флот///

Категория: Студенческий проект
Год: 2018
Типология: Приходской комплекс
Вместимость: 300-350 человек
Площадь участка: 2 800 кв.м.
Площадь застройки: 470 кв.м.

Инструменты

ArchiCAD, Blender, Cycles,
Photoshop


Храм приходского типа рассчитан на развитие локального сообщества верующих. Небольшой размер храма предполагает его размещение на узких участках, и использование в качестве приходского храма.

Этот проект — обращение к корням русской храмовой архитектуры через современные материалы и технологии строительства.

Образ храма опирается на ранний тип северных деревянных храмов с клинчатой кровлей. Этот тип характерен для русского севера, — региона, сохраняющего в себе древнейшие русские православные святыни.




Вид 1

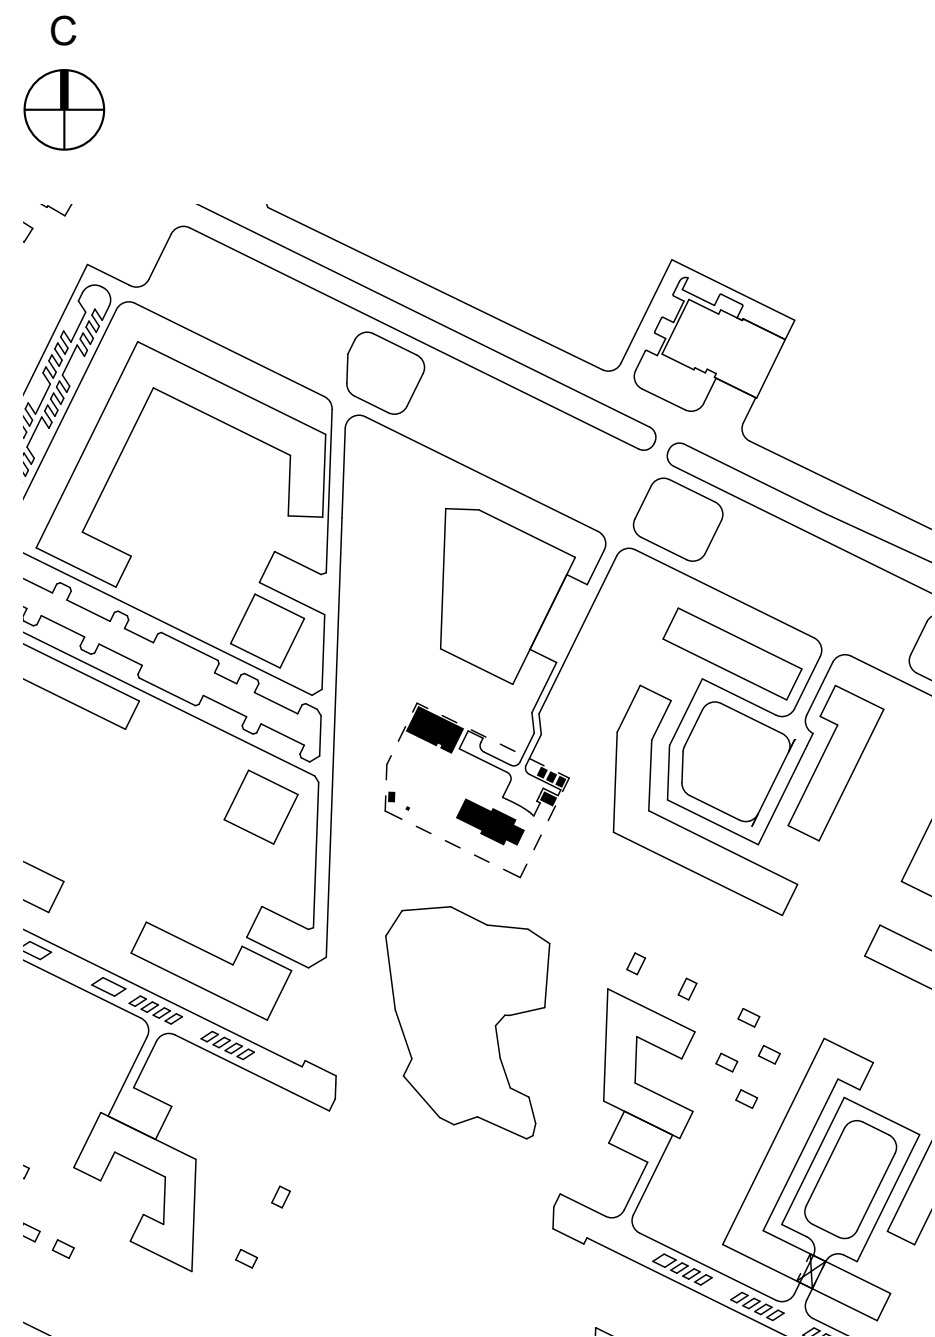


Ситуация

Проектируемый объект
расположен в жилом комплексе
(проектируемом ранее),
неподалеку от п.Ольгино,
г.Н.Новгород


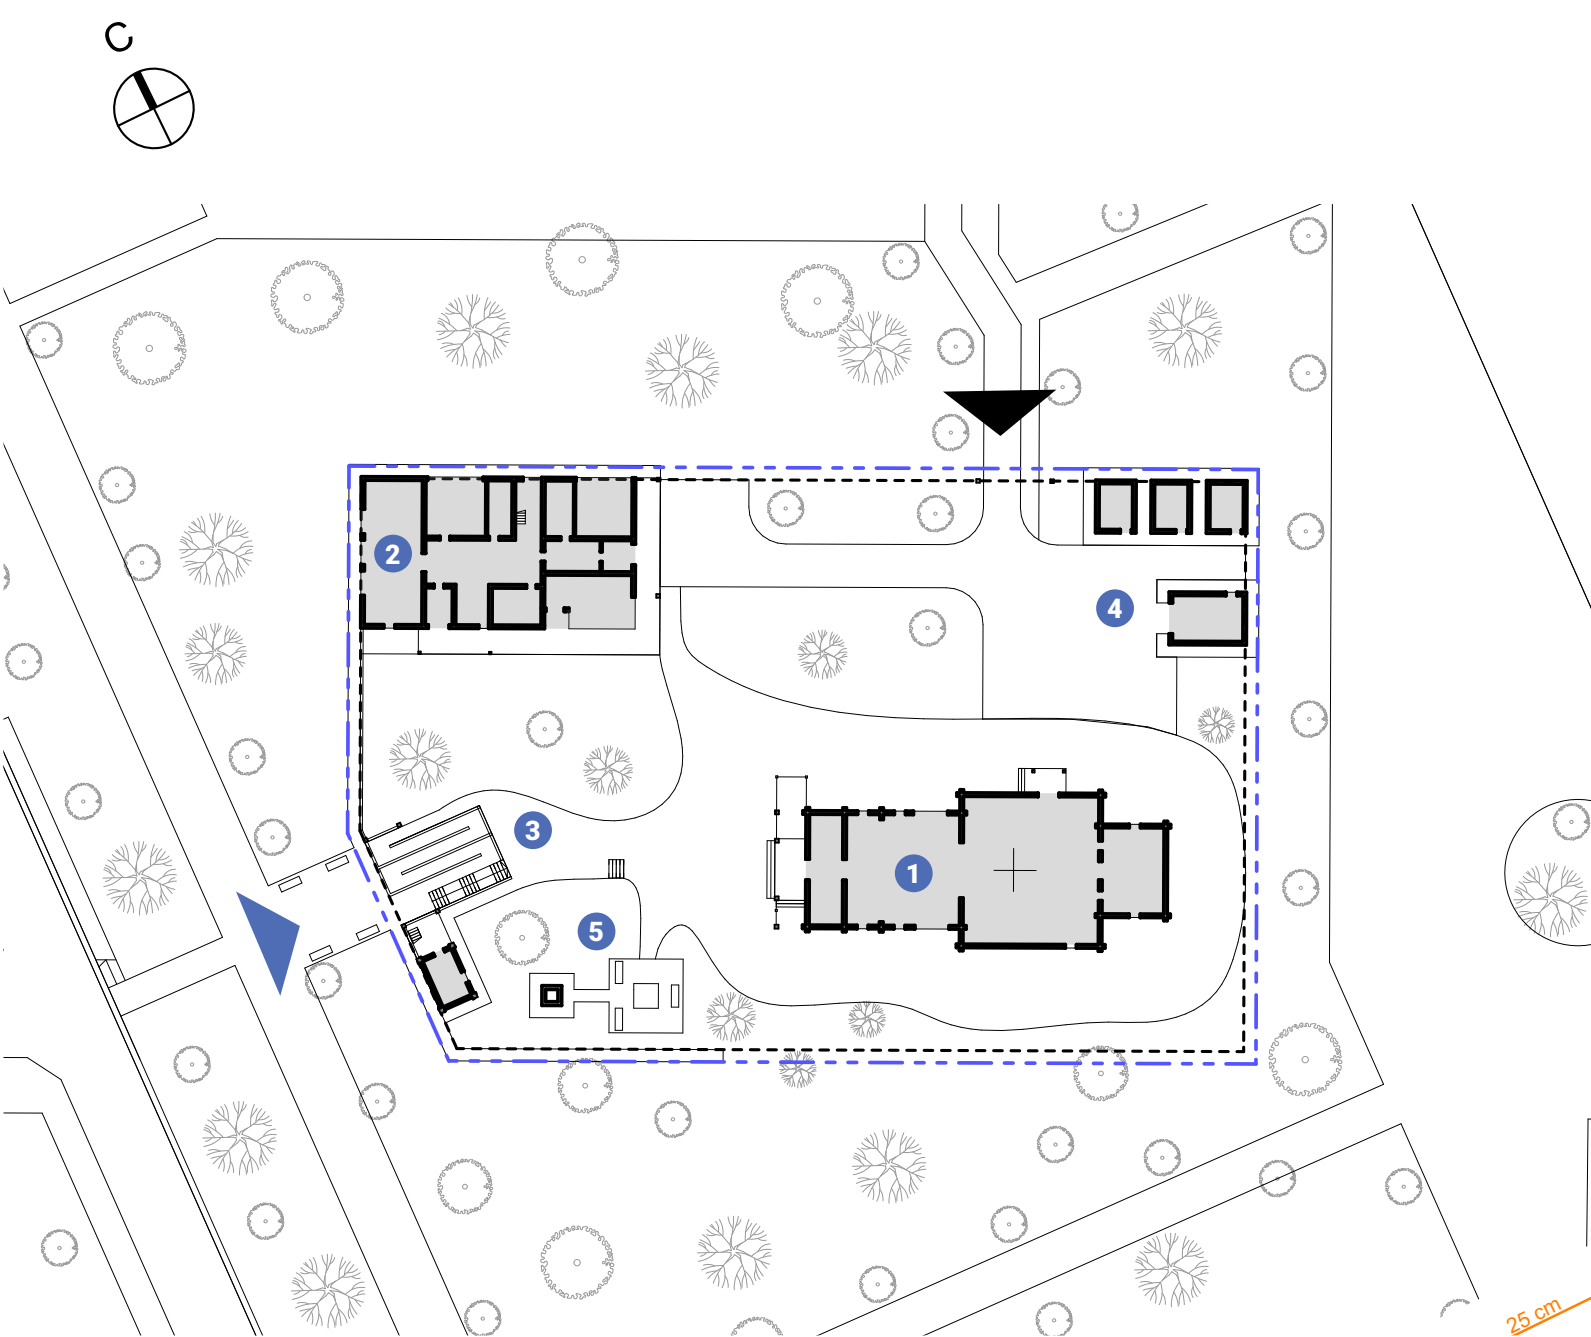


Генеральный план

- Экспликация:
- 1. Приходской храм
 - 2. Дом дьяка
 - 3. Входная группа со звонницей
 - 4. Гараж и мастерские
 - 5. Водосвятный колодец

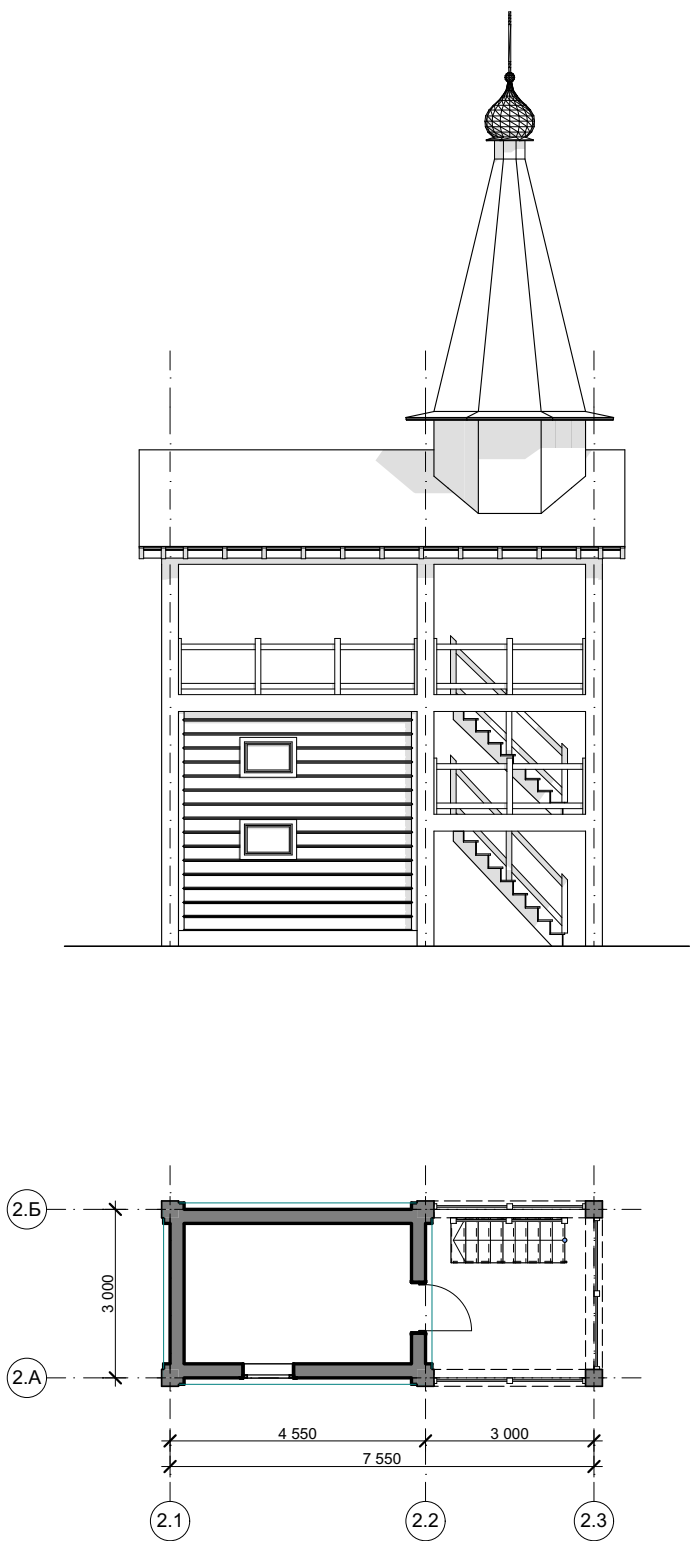

Звонница. Фасад и план

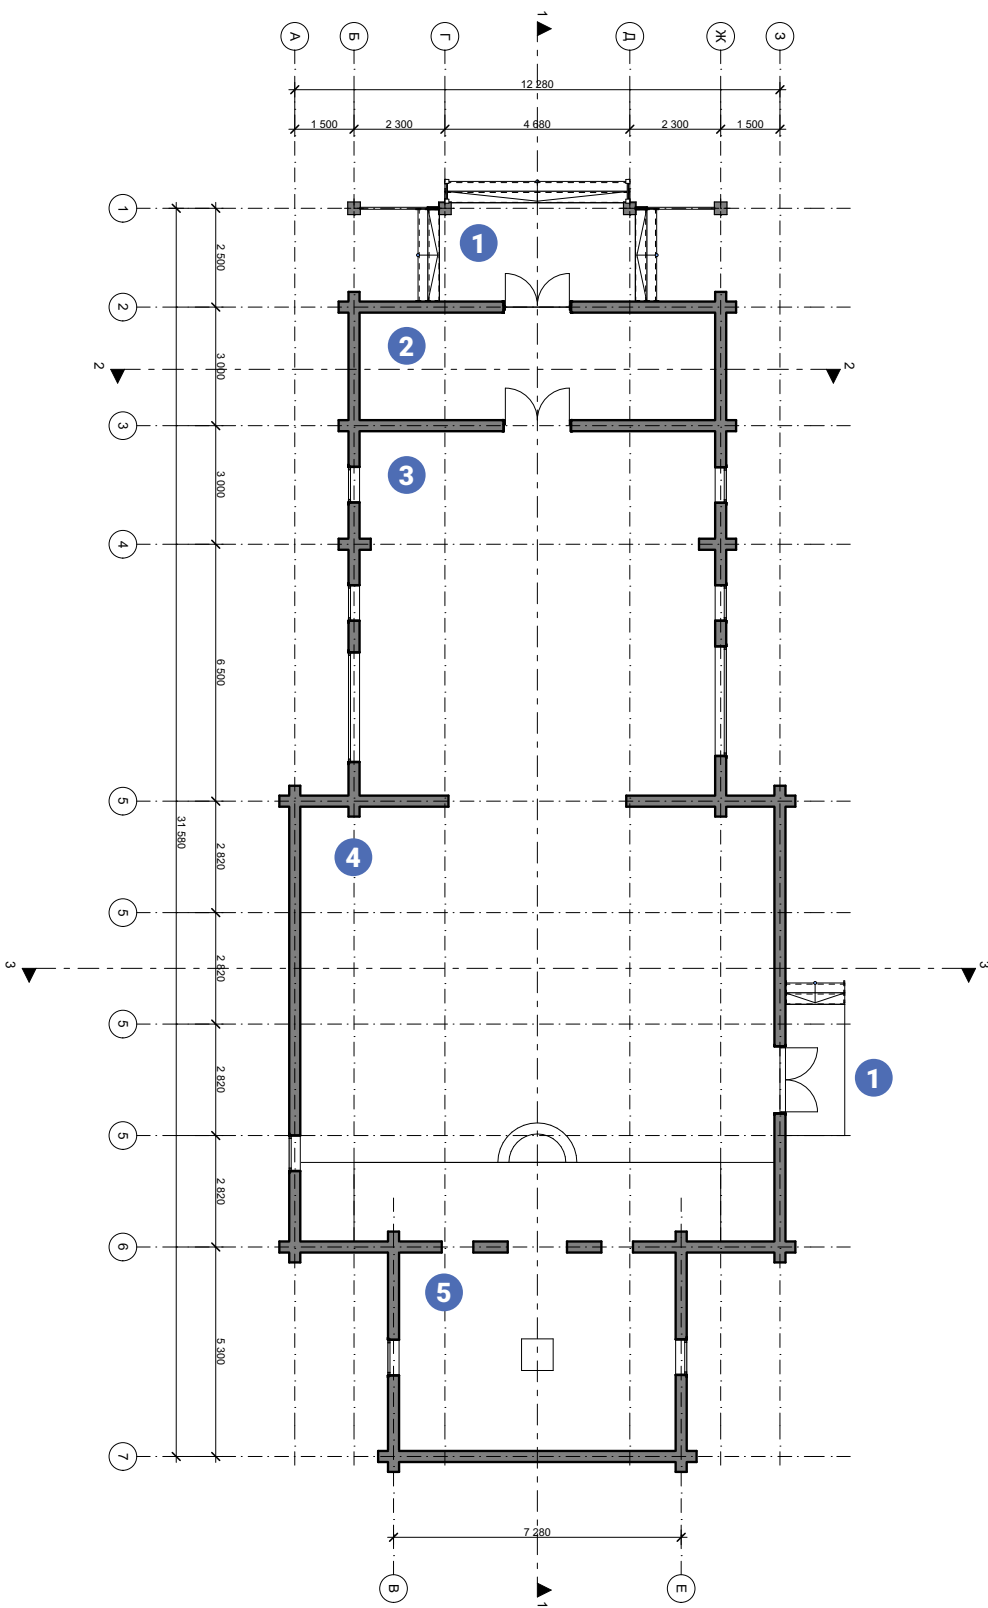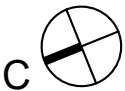


Экспликация:

- 1. Паперть, 8 + 5 кв.м.
- 2. Тамбур, 27 кв.м.
- 3. Притвор, 86 кв.м.
- 4. Храм, 100 кв.м.
- 5. Алтарь, 36 кв.м.

Церковь. План






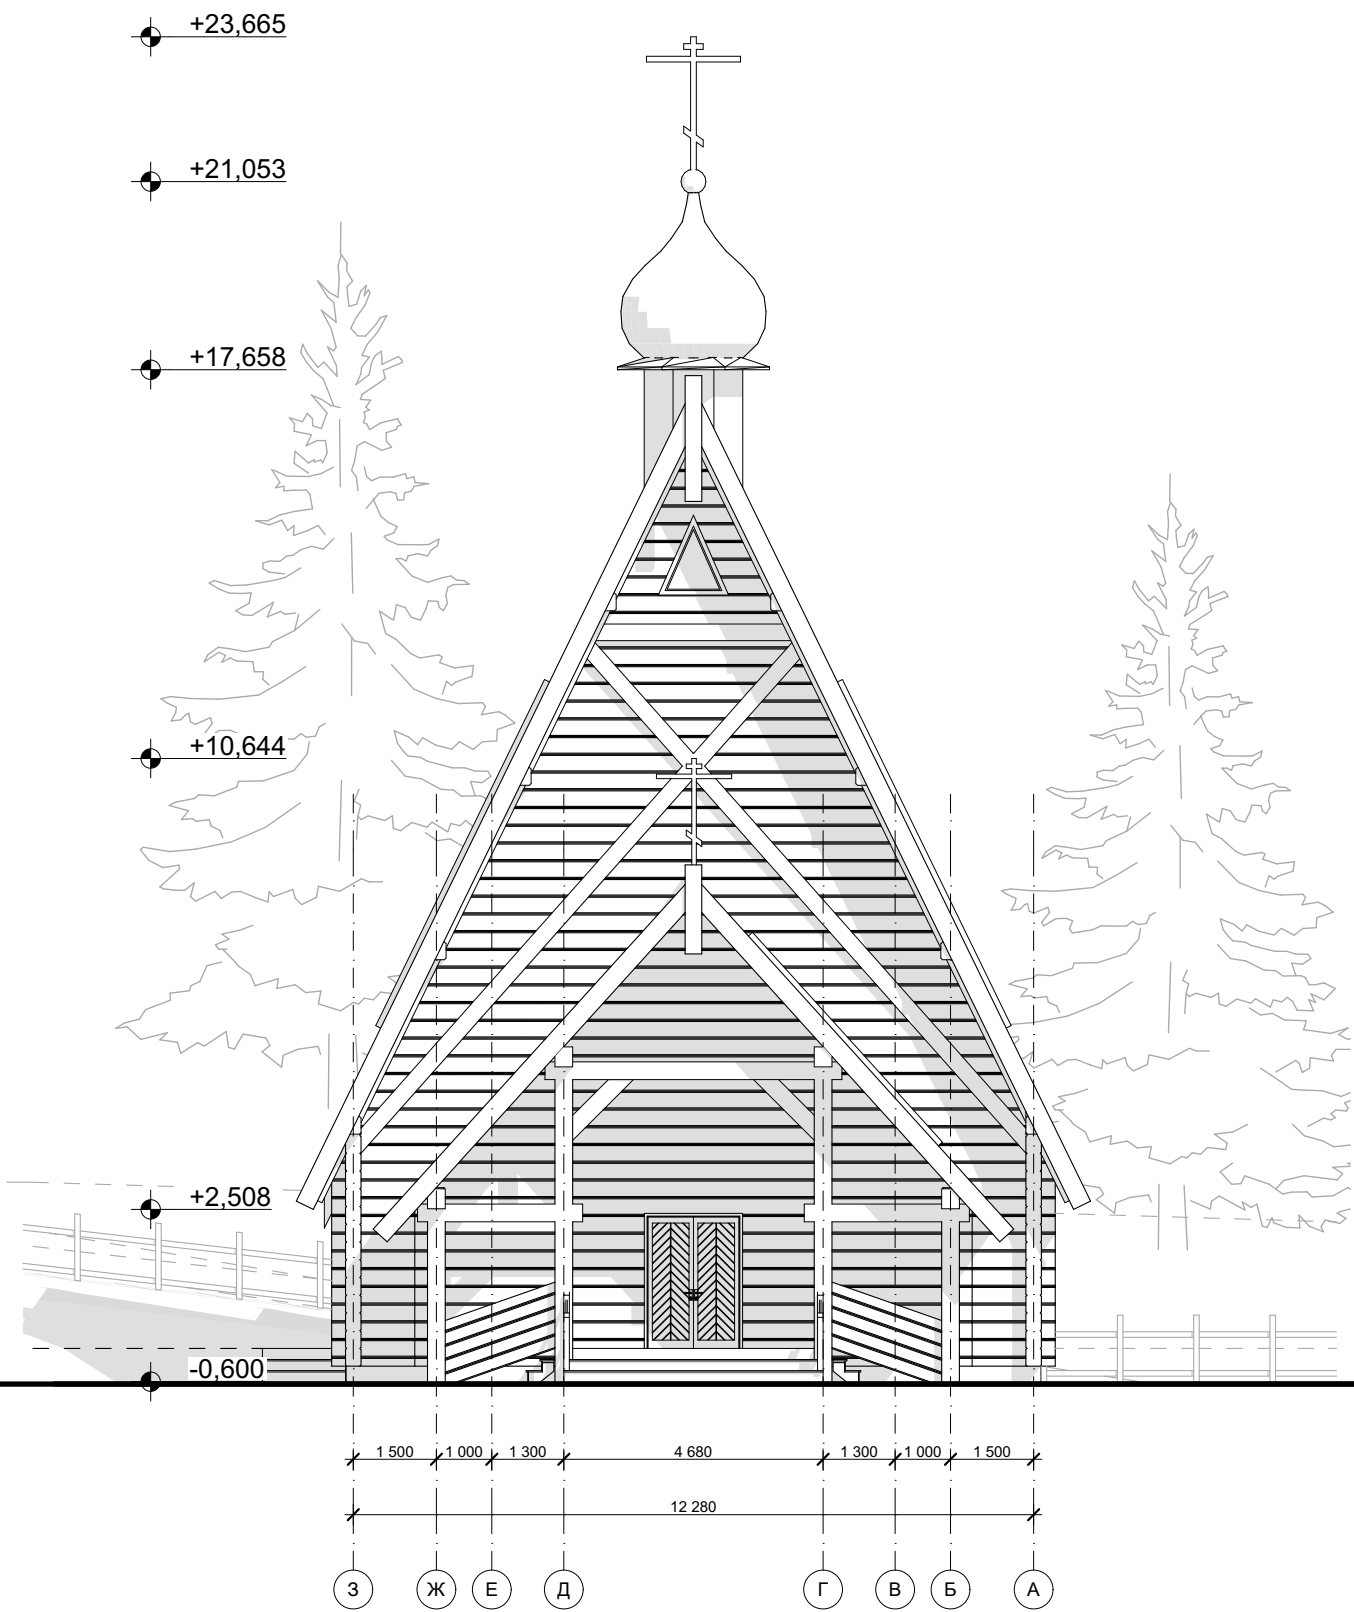


Церковь. Фасад в осях 3-А




Церковь. Разрез 3-3



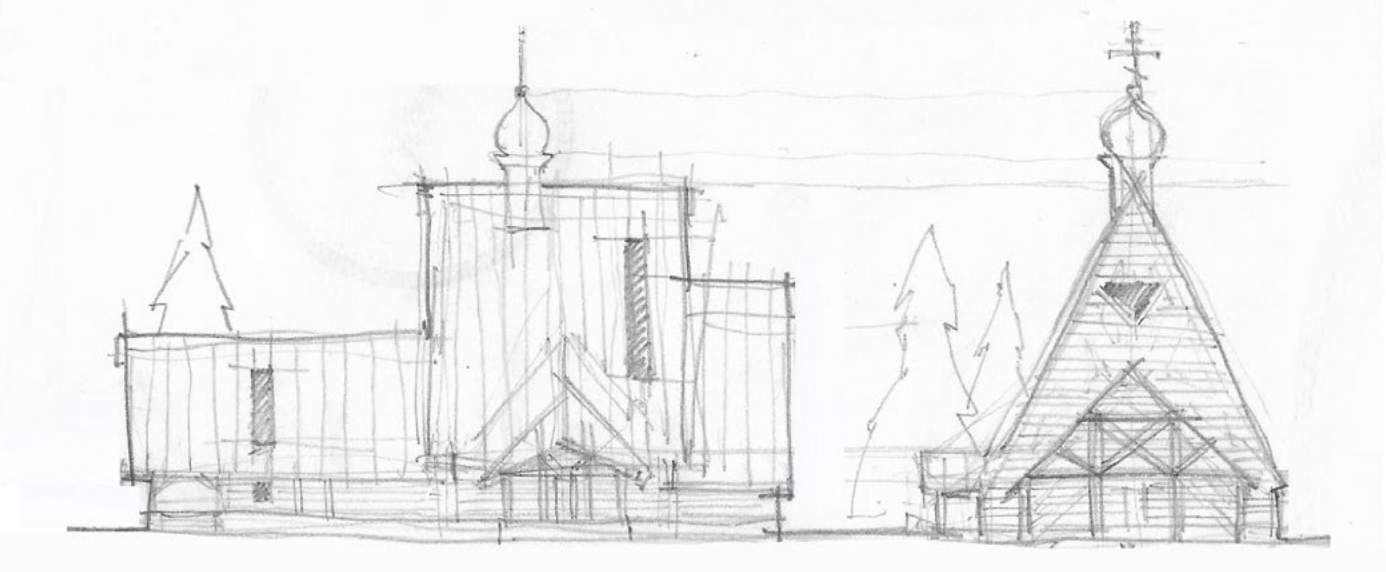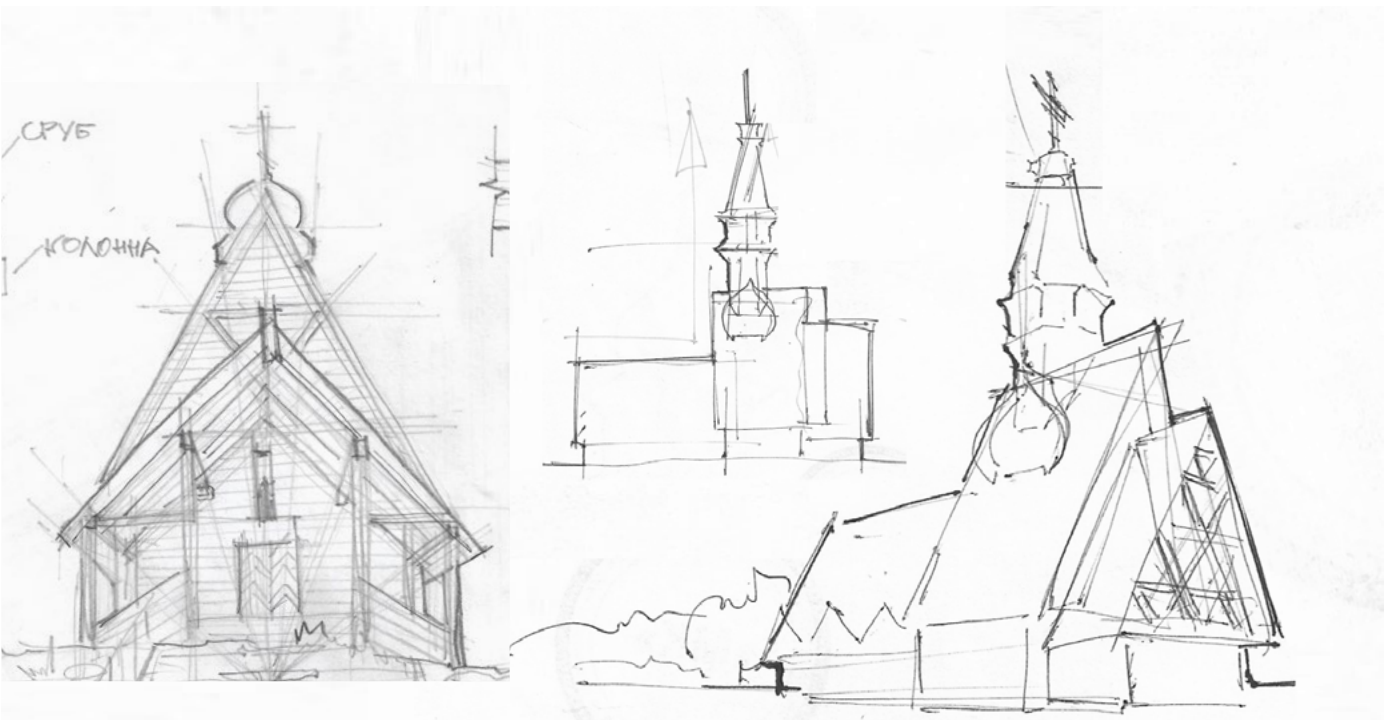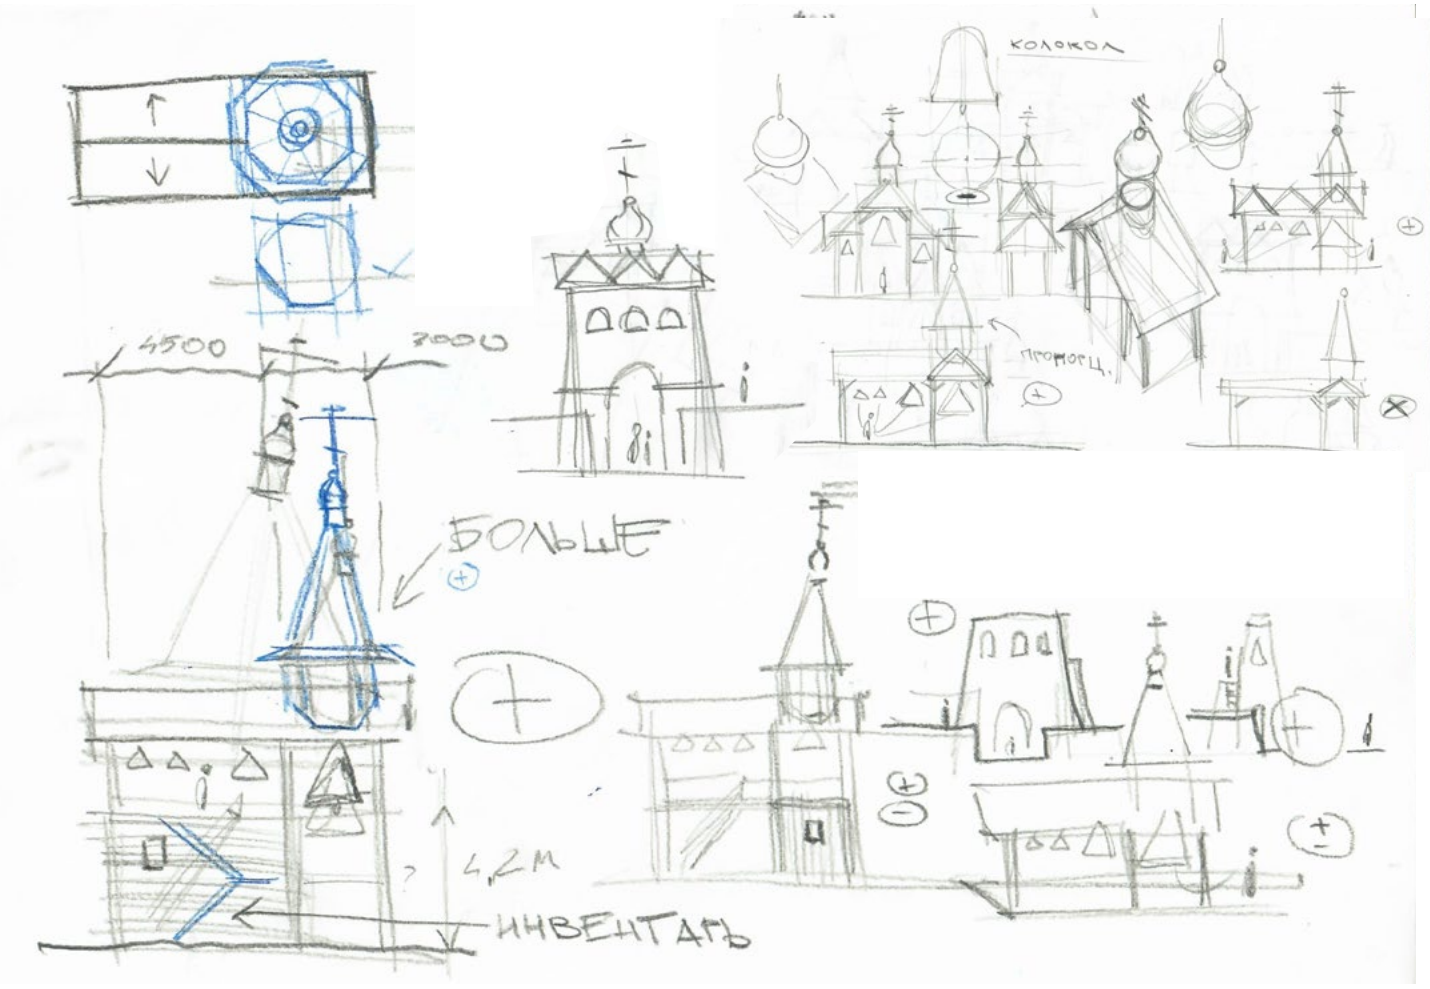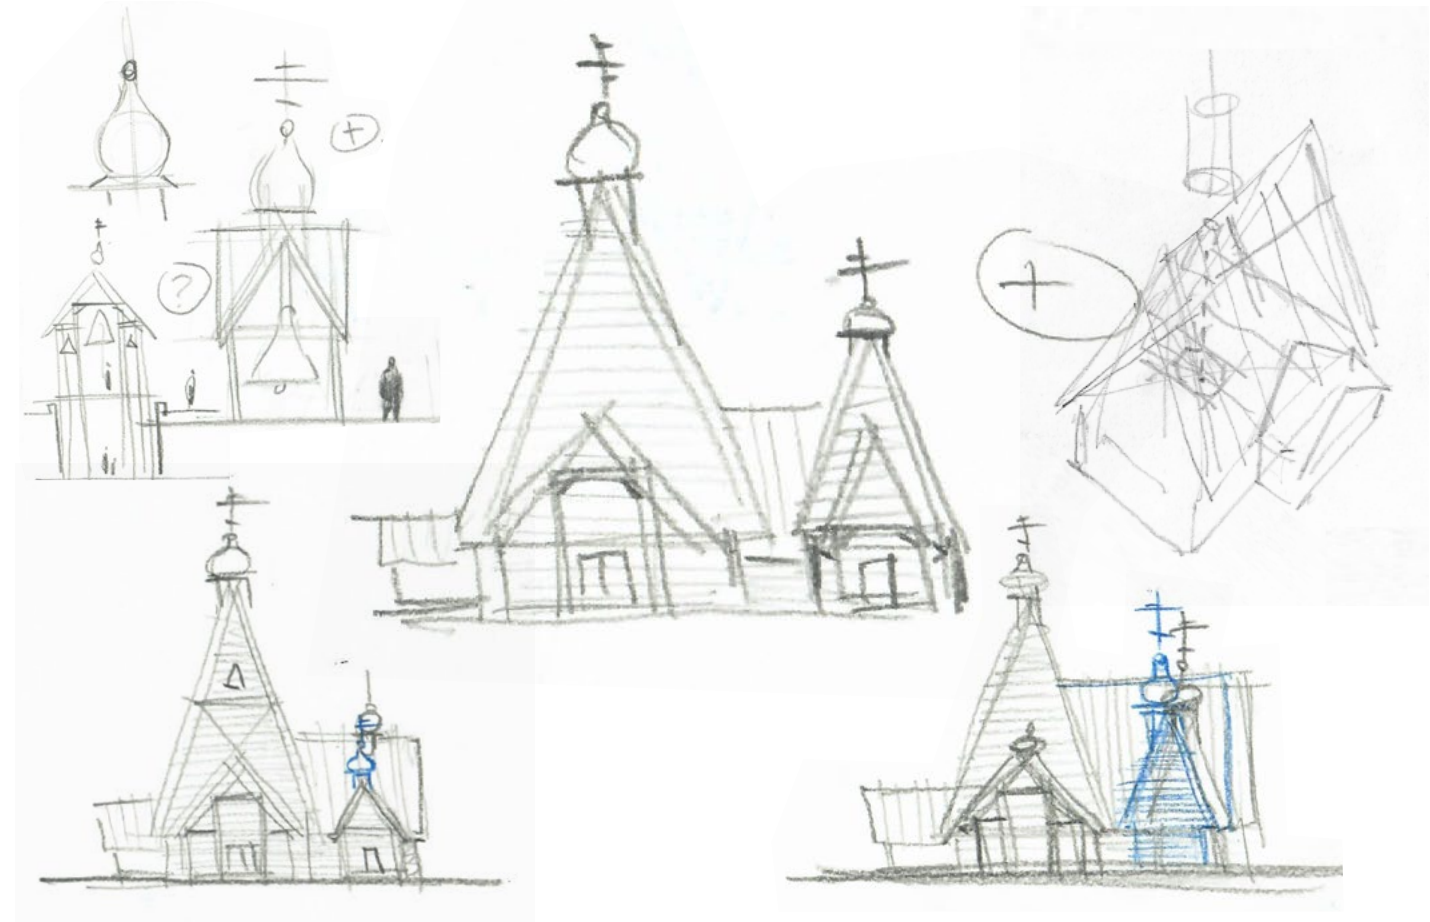

ВМЕСТИМОСТЬ ХРАМА
300-350 чел - по ТЗ
мин. 450 чел - по СП
60 тыс. чел. населения

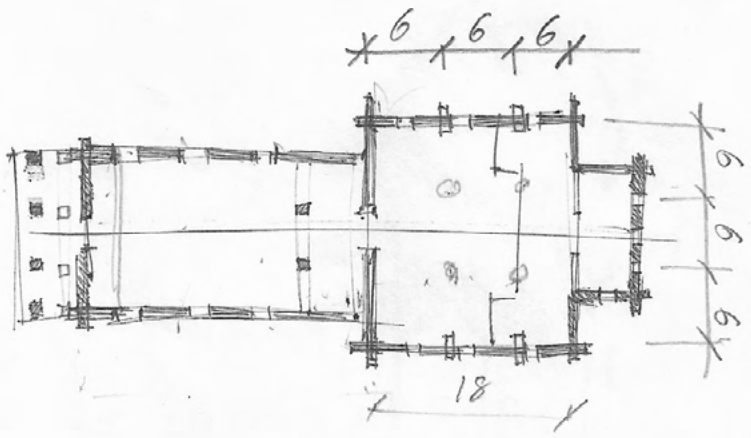

жк_королёв///

Категория: Коммерческий проект
Проектная организация: ЗАО "Межрегиональный Институт Градостроительства"
Заказчик: Комитет по архитектуре и градостроительству города Москвы
Год: 2018
Типология: Жилой комплекс
Планируемое население: 2 256 человек
Пл. участка: 60 000 кв.м.
Роль в проекте: Разработка фасадной концепции, контроль дизайн-составляющей, выдача ТЗ на визуализацию

Инструменты

AutoCAD, ArchiCAD, SketchUp, Photoshop, Illustrator, графический планшет

Фасадные решения предлагаемой застройки формируют выразительный и узнаваемый образ. Переменная этажность позволяет создать оригинальный силуэт жилых домов и избежать однообразности при визуальном

восприятию застройки. Фактурной и цветовой основой всего жилого комплекса является отделка фасадов темно-серым кирпичом. Композиционное равновесие доминирующих по массе и высоте угловых секций с


типовыми секциями достигается с помощью объединяющих элементов и цветовых переходов.








Фрагмент эскизного предложения планировочного решения территории.

*Автор портфолио не является разработчиком представленной 3D-визуализации

ОБРАЗ КИНОМЕНТЫ

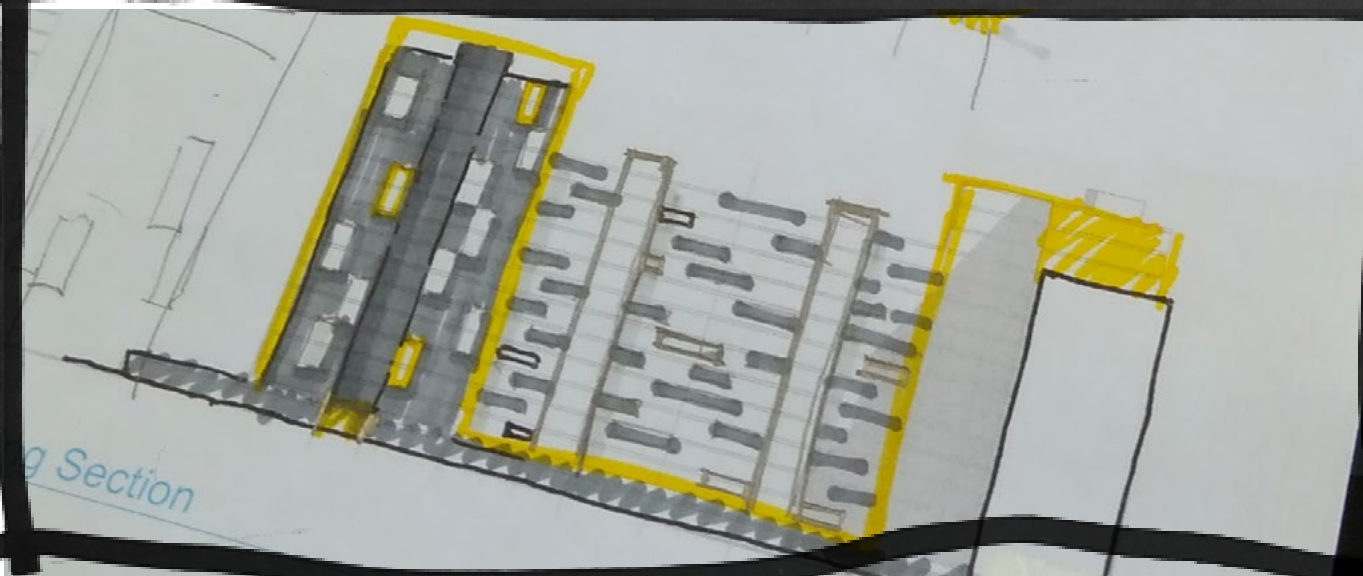


Поиск фасадной **концепции** жилых домов.
/ Первые несколько вариантов.

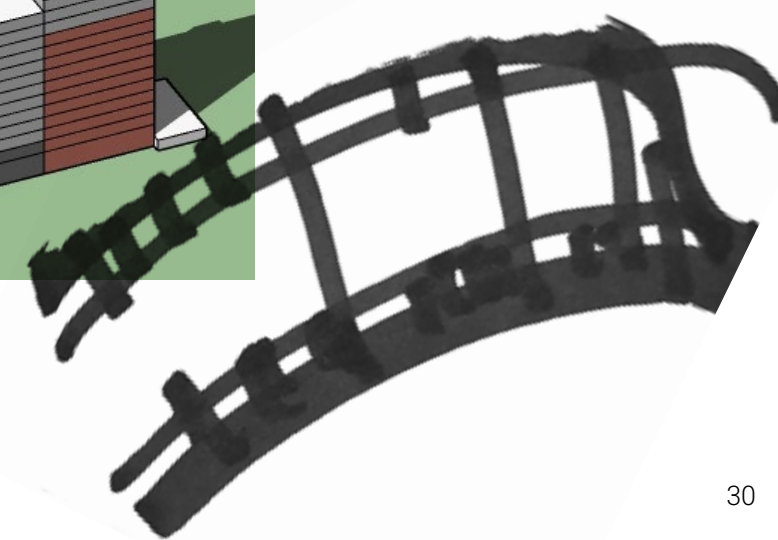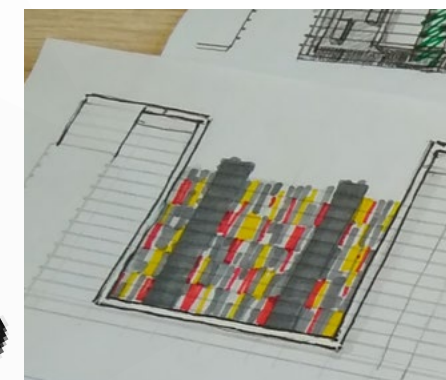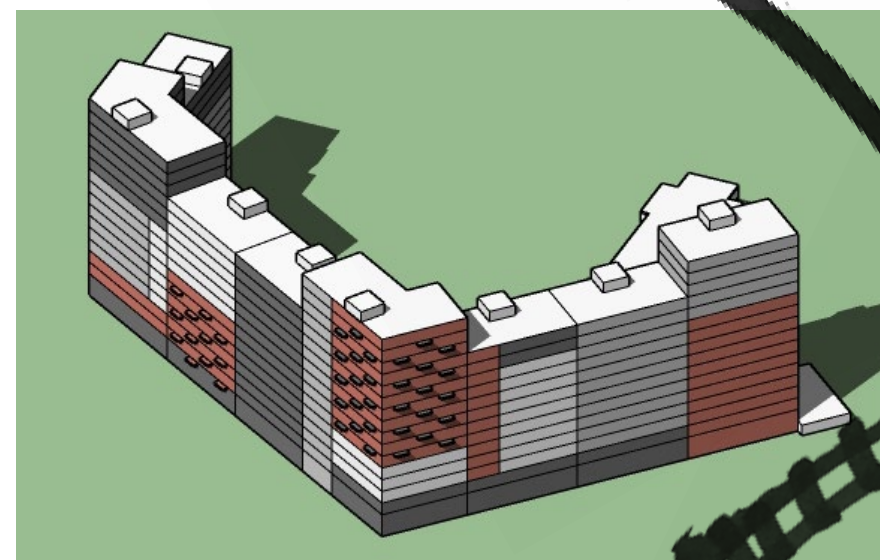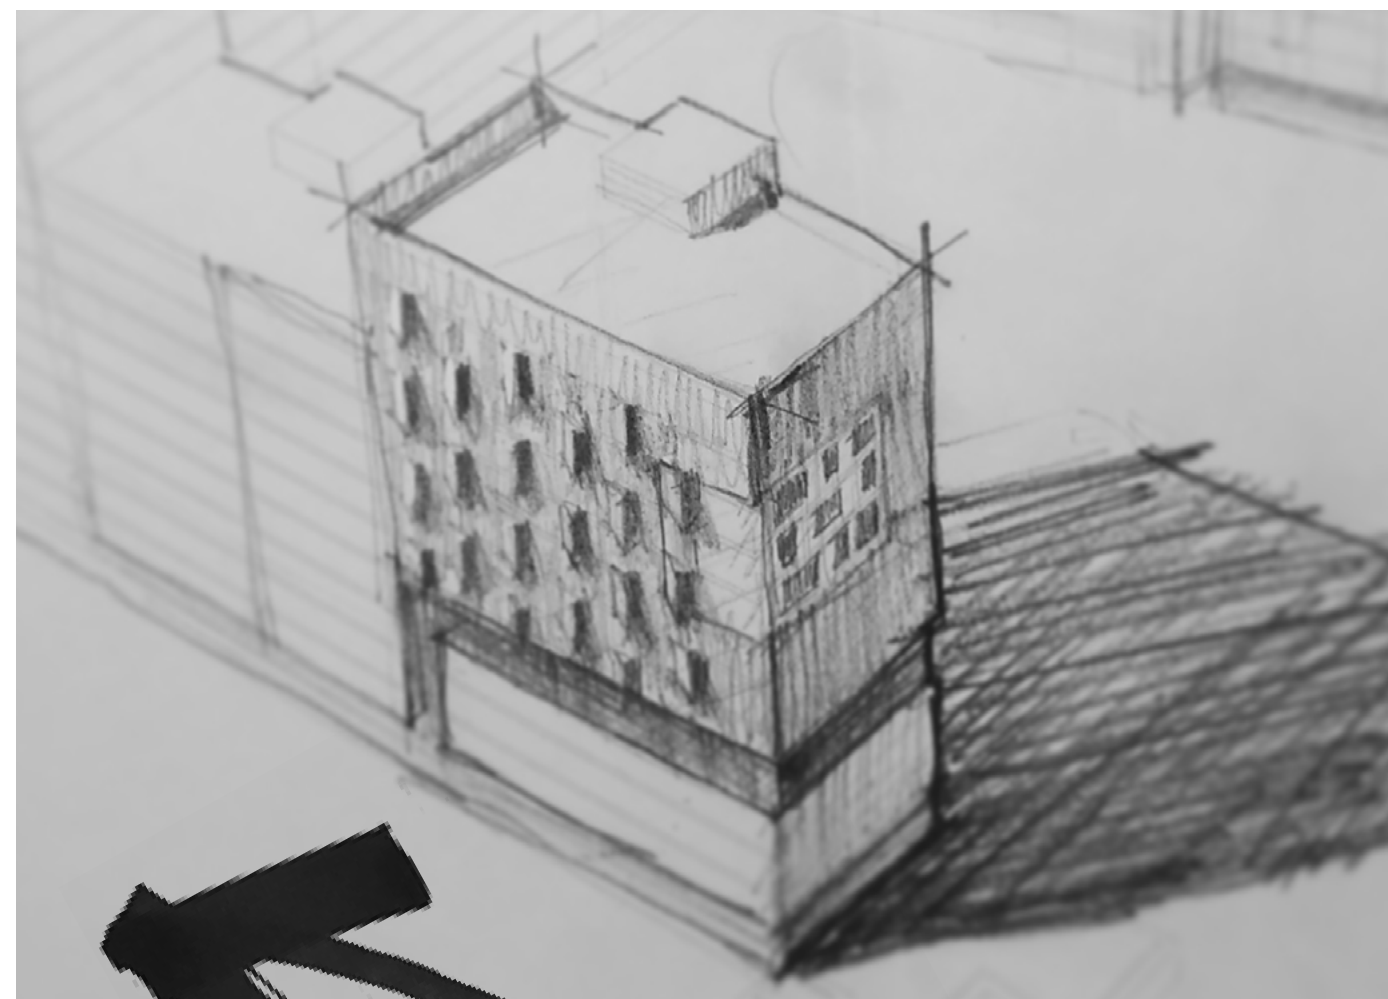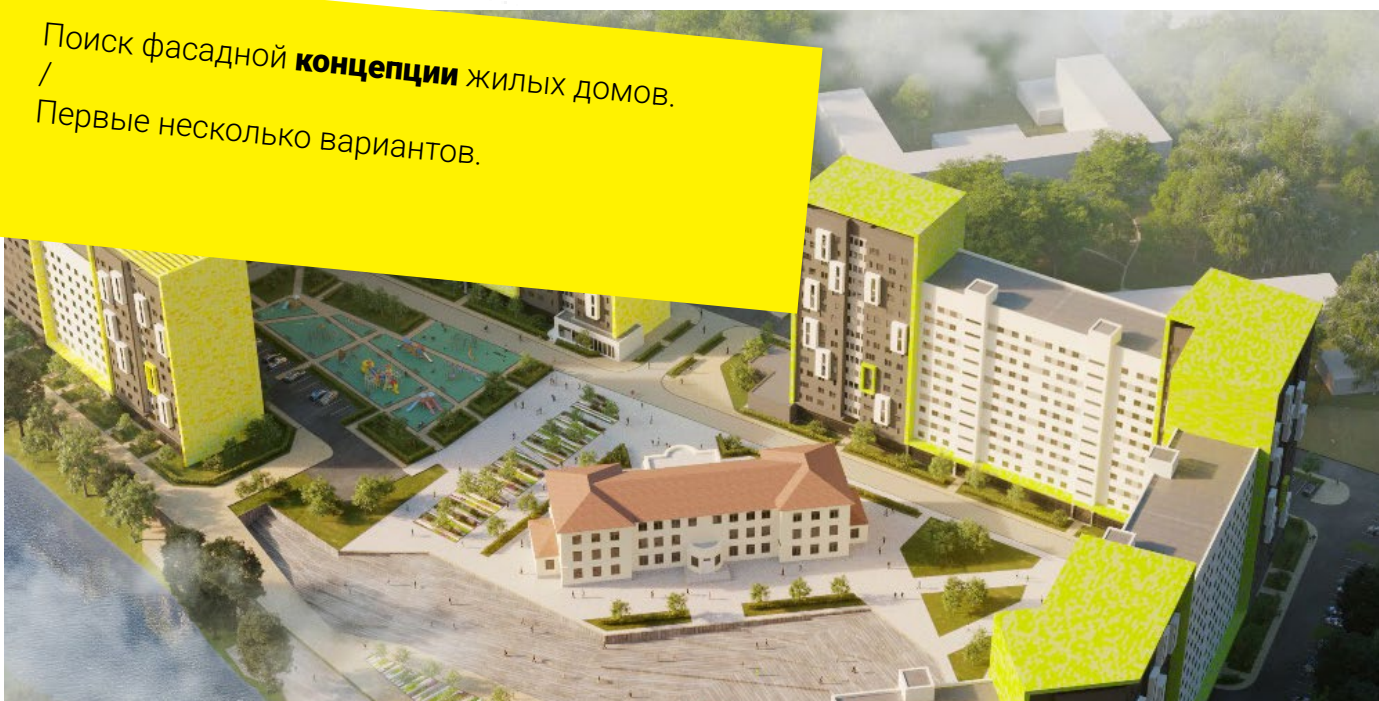



Школа искусств. Фасад главный

Одной из основных задач проекта - представить, как могла быть выглядеть территория и фасады бывшего Дома творчества союза кинематографистов СССР после реконструкции. Выше представлены главный и боковой фасады здания.

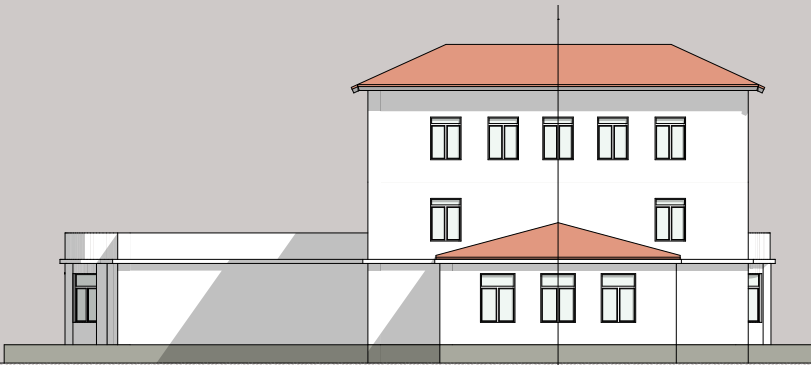

Школа искусств. Фасад торцевой




ДОУ. Фасад главный



ДОУ. Фасад торцевой

Была разработана дизайн-концепция фасадов ДОУ, расположенного на территории будущего комплекса. Планировочное решение здания ДОУ предоставлено организацией-заказчиком.

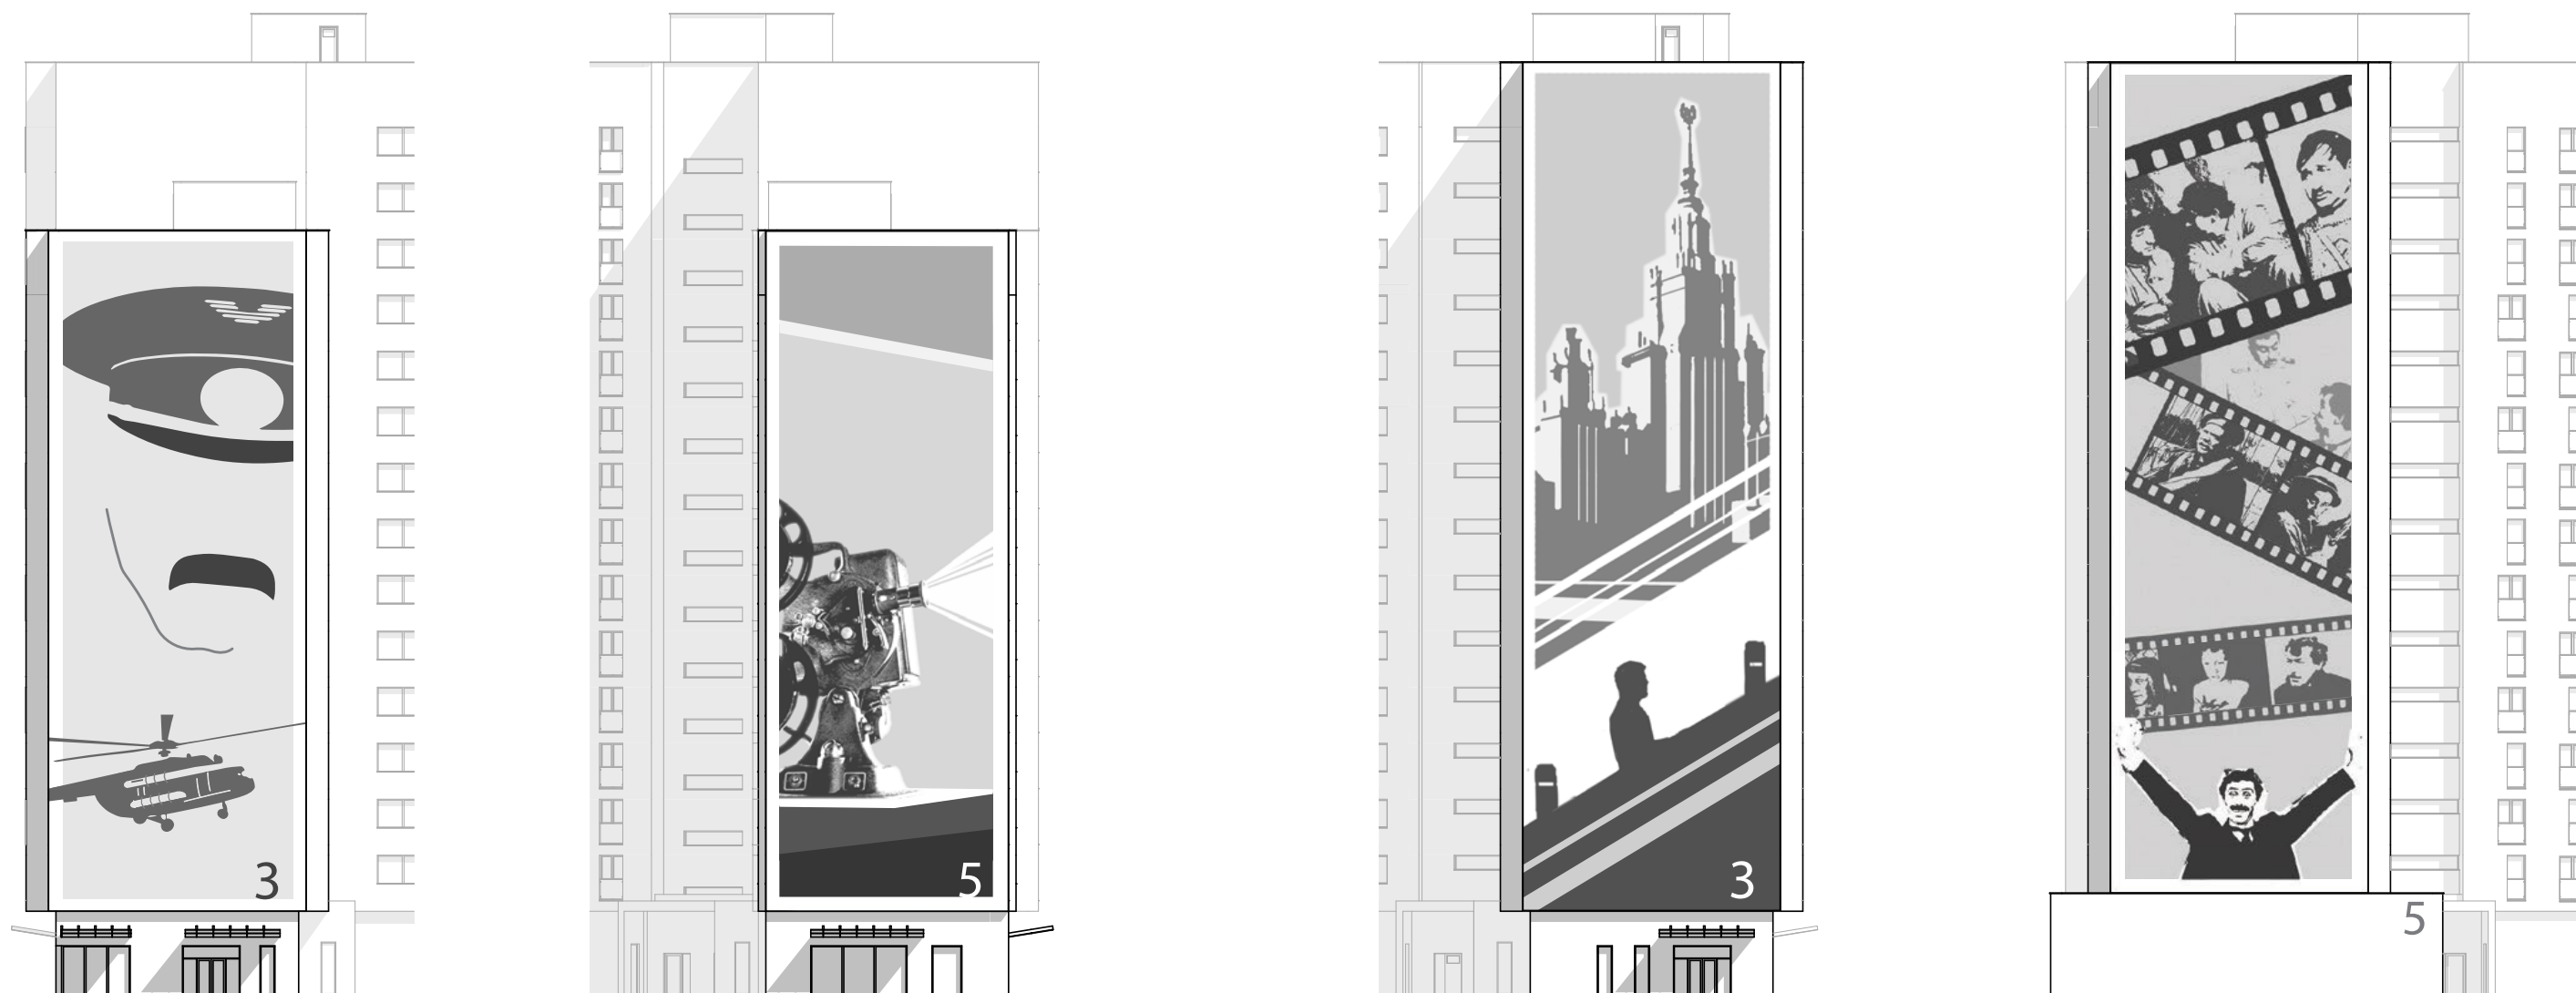

Предложение по художественному оформлению торцевых фасадов

Поскольку в основе дизайн-концепции комплекса положена тема творчества союза кинематографистов, было решено оформить торцевые фасады жилых домов в виде минималистичных плакатов к советскому кино.

*Автор портфолио не является
разработчиком демонстрируемой
3D-визуализации



эффект_бабочки///



Полное название:	Реконструкция транспортной развязки метро Пролетарская в г.Нижнем Новгороде
Категория:	Бакалаврская ВКР
Год:	2020
Типология:	Общественное пространство + многофункциональная застройка
Вместимость жилья:	17 500 человек
Площадь участка:	109 Га

Целью работы являются выявление возможного направления развития транспортной развязки станции метро Пролетарская а также её примыкающих территорий с учетом прогнозного по генеральному плану города Нижнего Новгорода.


Инструменты

ArchiCAD, Blender 3D, Photoshop, Illustrator, графический планшет

//предпроектный_анализ

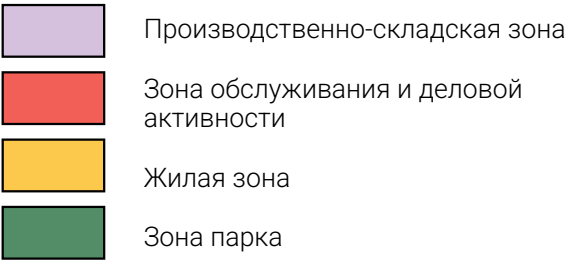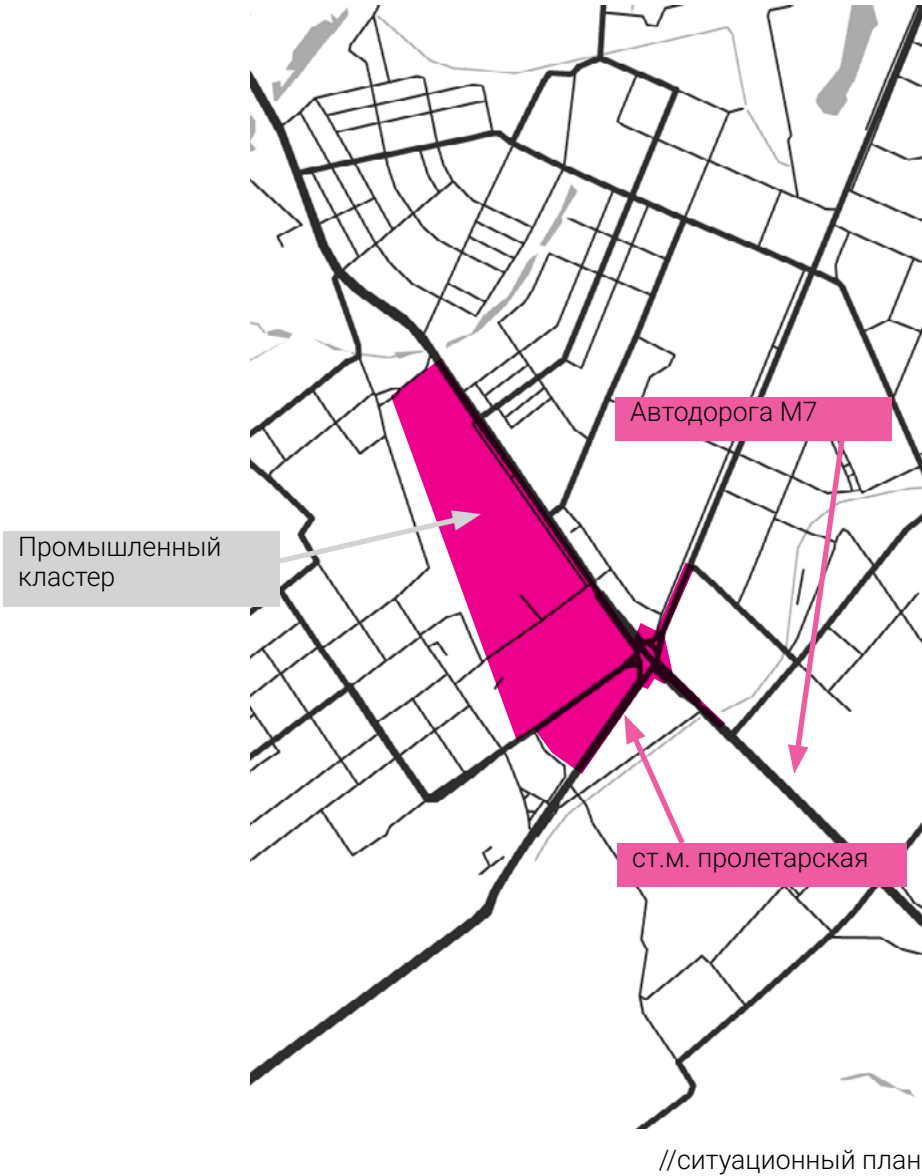



//фрагмент схемы функционального зонирования города

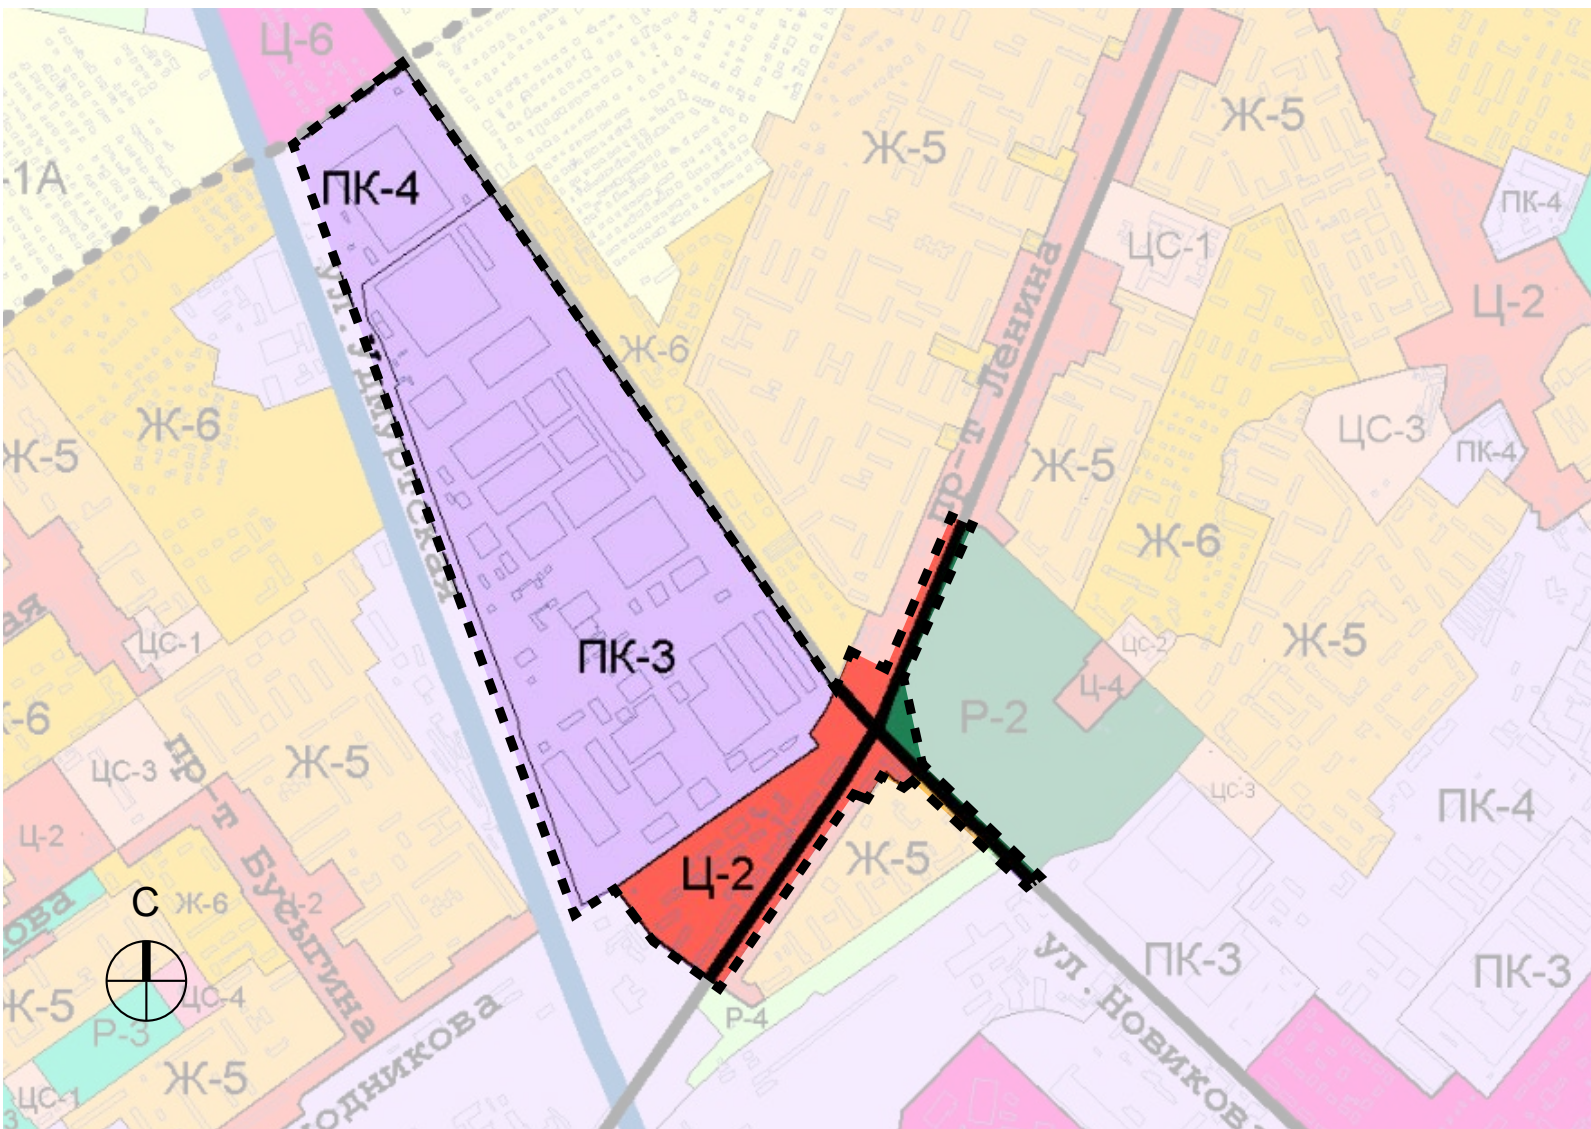


Задачи:

- » Анализ на возможность приспособления участка трассы М7 «Волга» в районе ст. метро «Пролетарская» и прилегающего транспортно-пешеходного узла под современные стандарты комфортной городской среды;
- » Урегулирование транспортной ситуации на участке;
- » Усовершенствовать пешеходную связь развязки с парком «Дубки»;
- » ликвидация диссонирующей застройки и преобразование её в жильё и места приложения труда;
- » Улучшение экологической ситуации;

Использование земли, в % от всего (глубокий анализ)

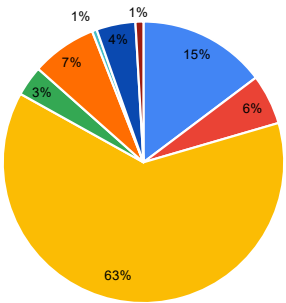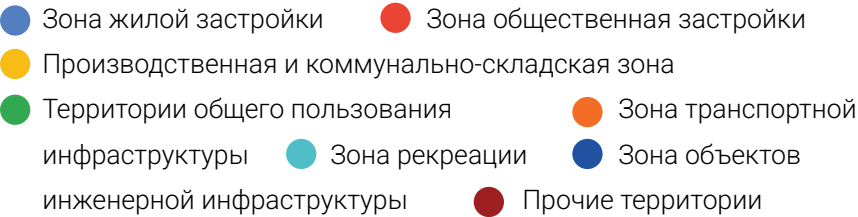



//_проектное_предложение

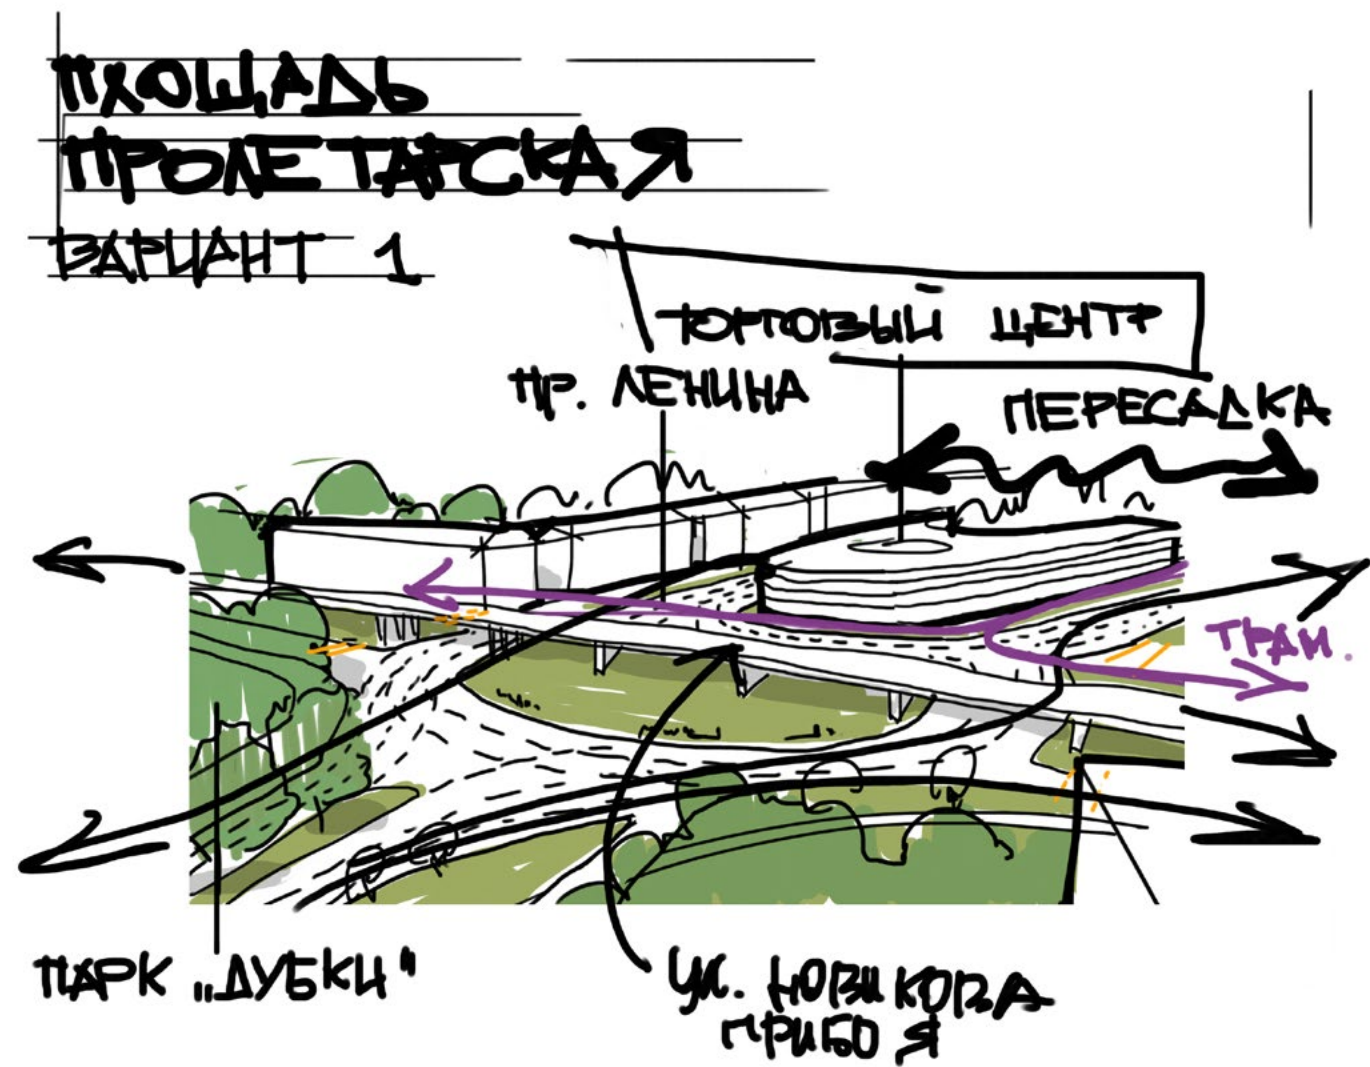

Концепция №1 - Концепция минимальных вложений - предполагает комплекс мероприятий из: 1) возврата кругового движения на участке; 2) демонтажа диссонирующей застройки и строительство на её месте многофункционального комплекса; 3) благоустройства прилегающих территорий




Концепция №2 - концепция максимум.
Согласно ей, помимо предшествующих мероприятий, предлагается строительство 2х жилых микрорайонов на месте ликвидируемого промышленного кластера, а также строительство пешеходного виадука, связывающего парк Дубки с комплексом зданий при станции метро.
В основу архитектурно-дизайнерской мысли пешеходной развязки положен **образ бабочки.**

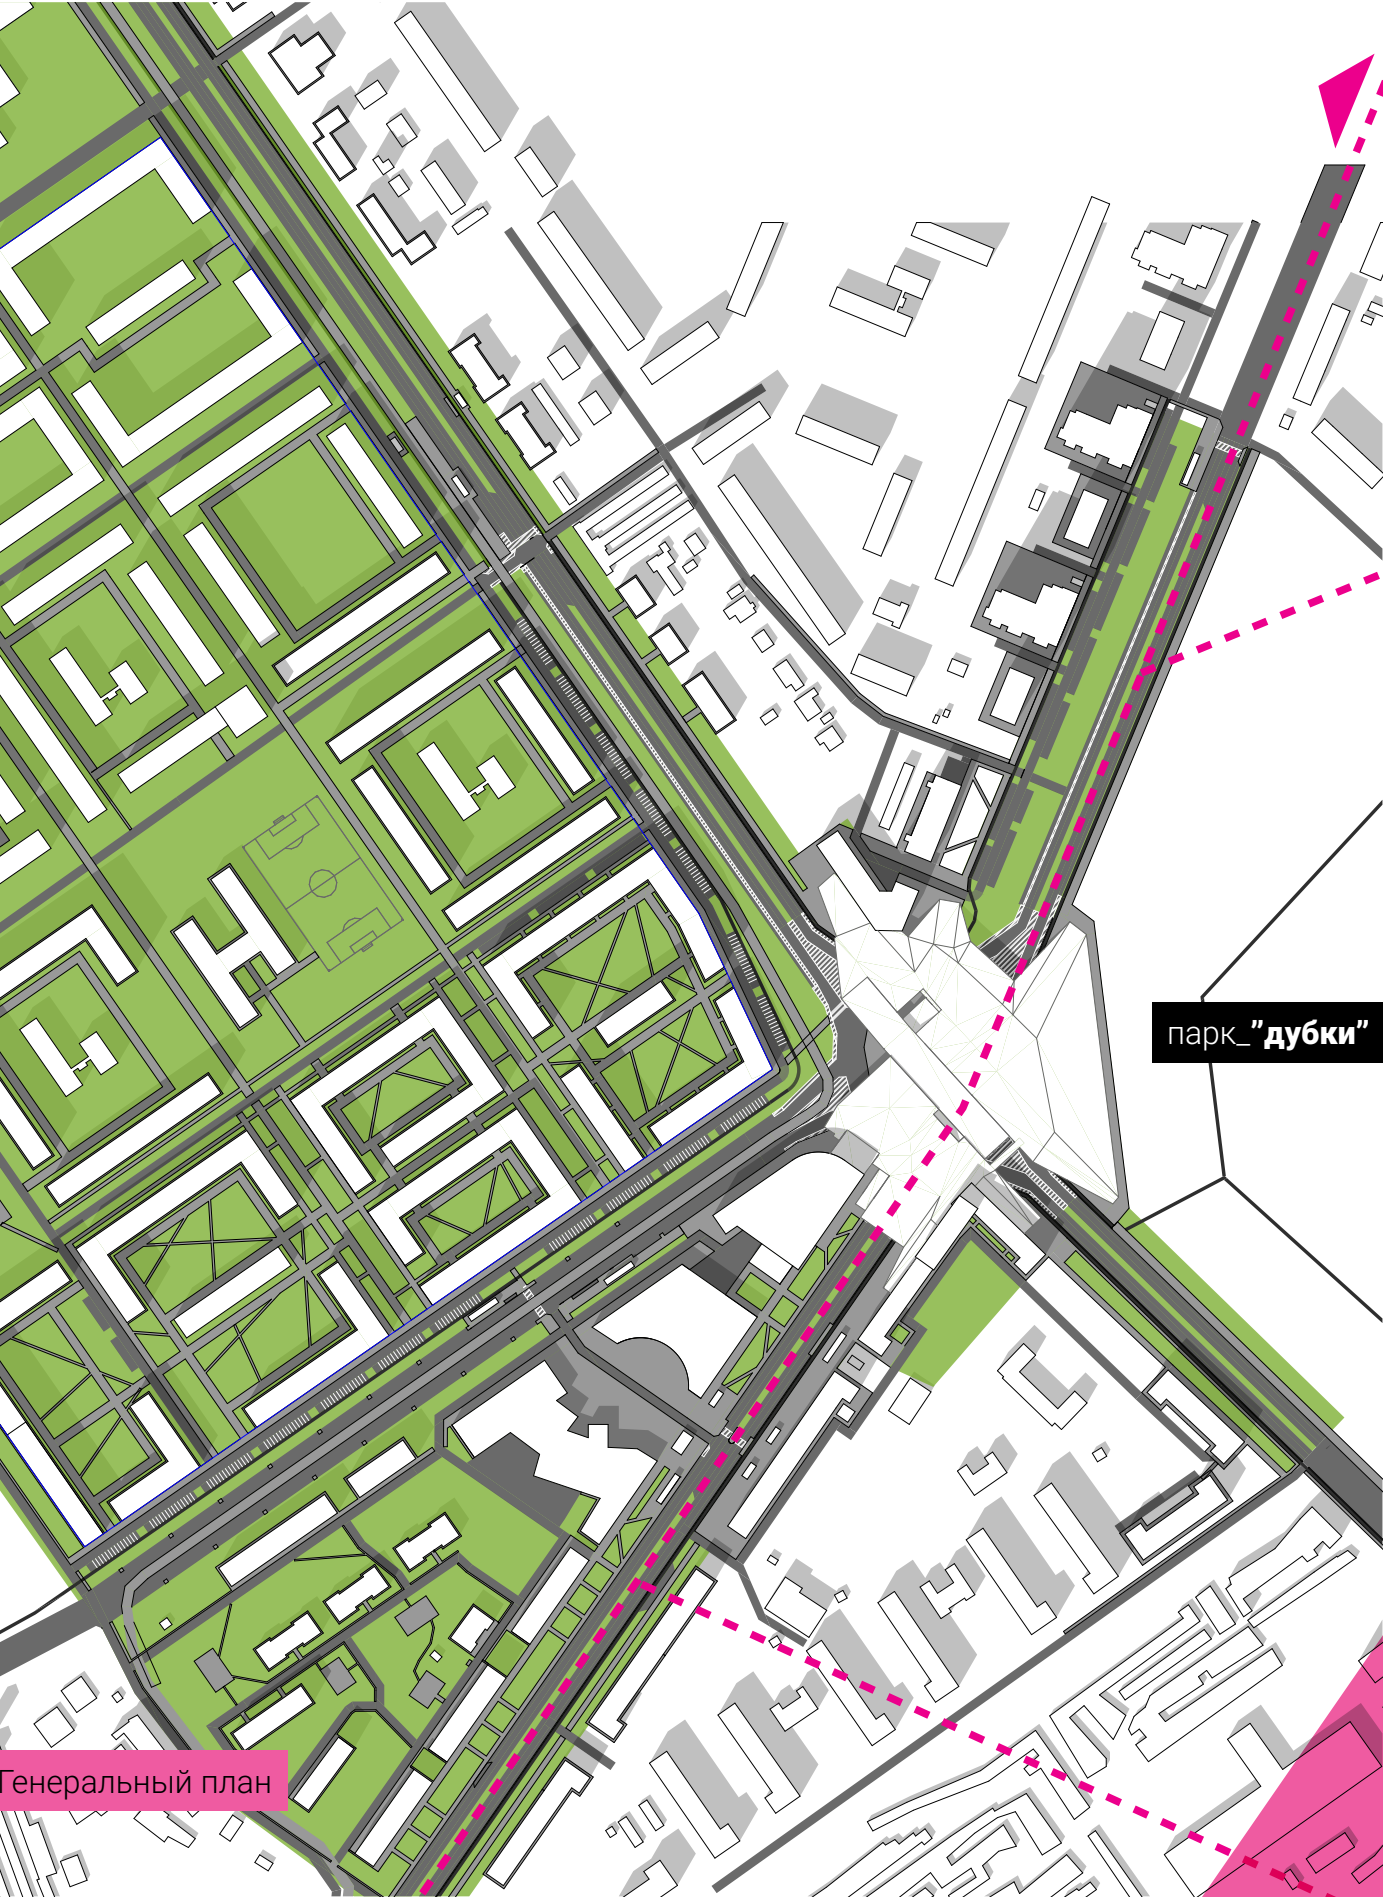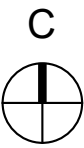

Генеральный план


Развертка по проспекту Ленина

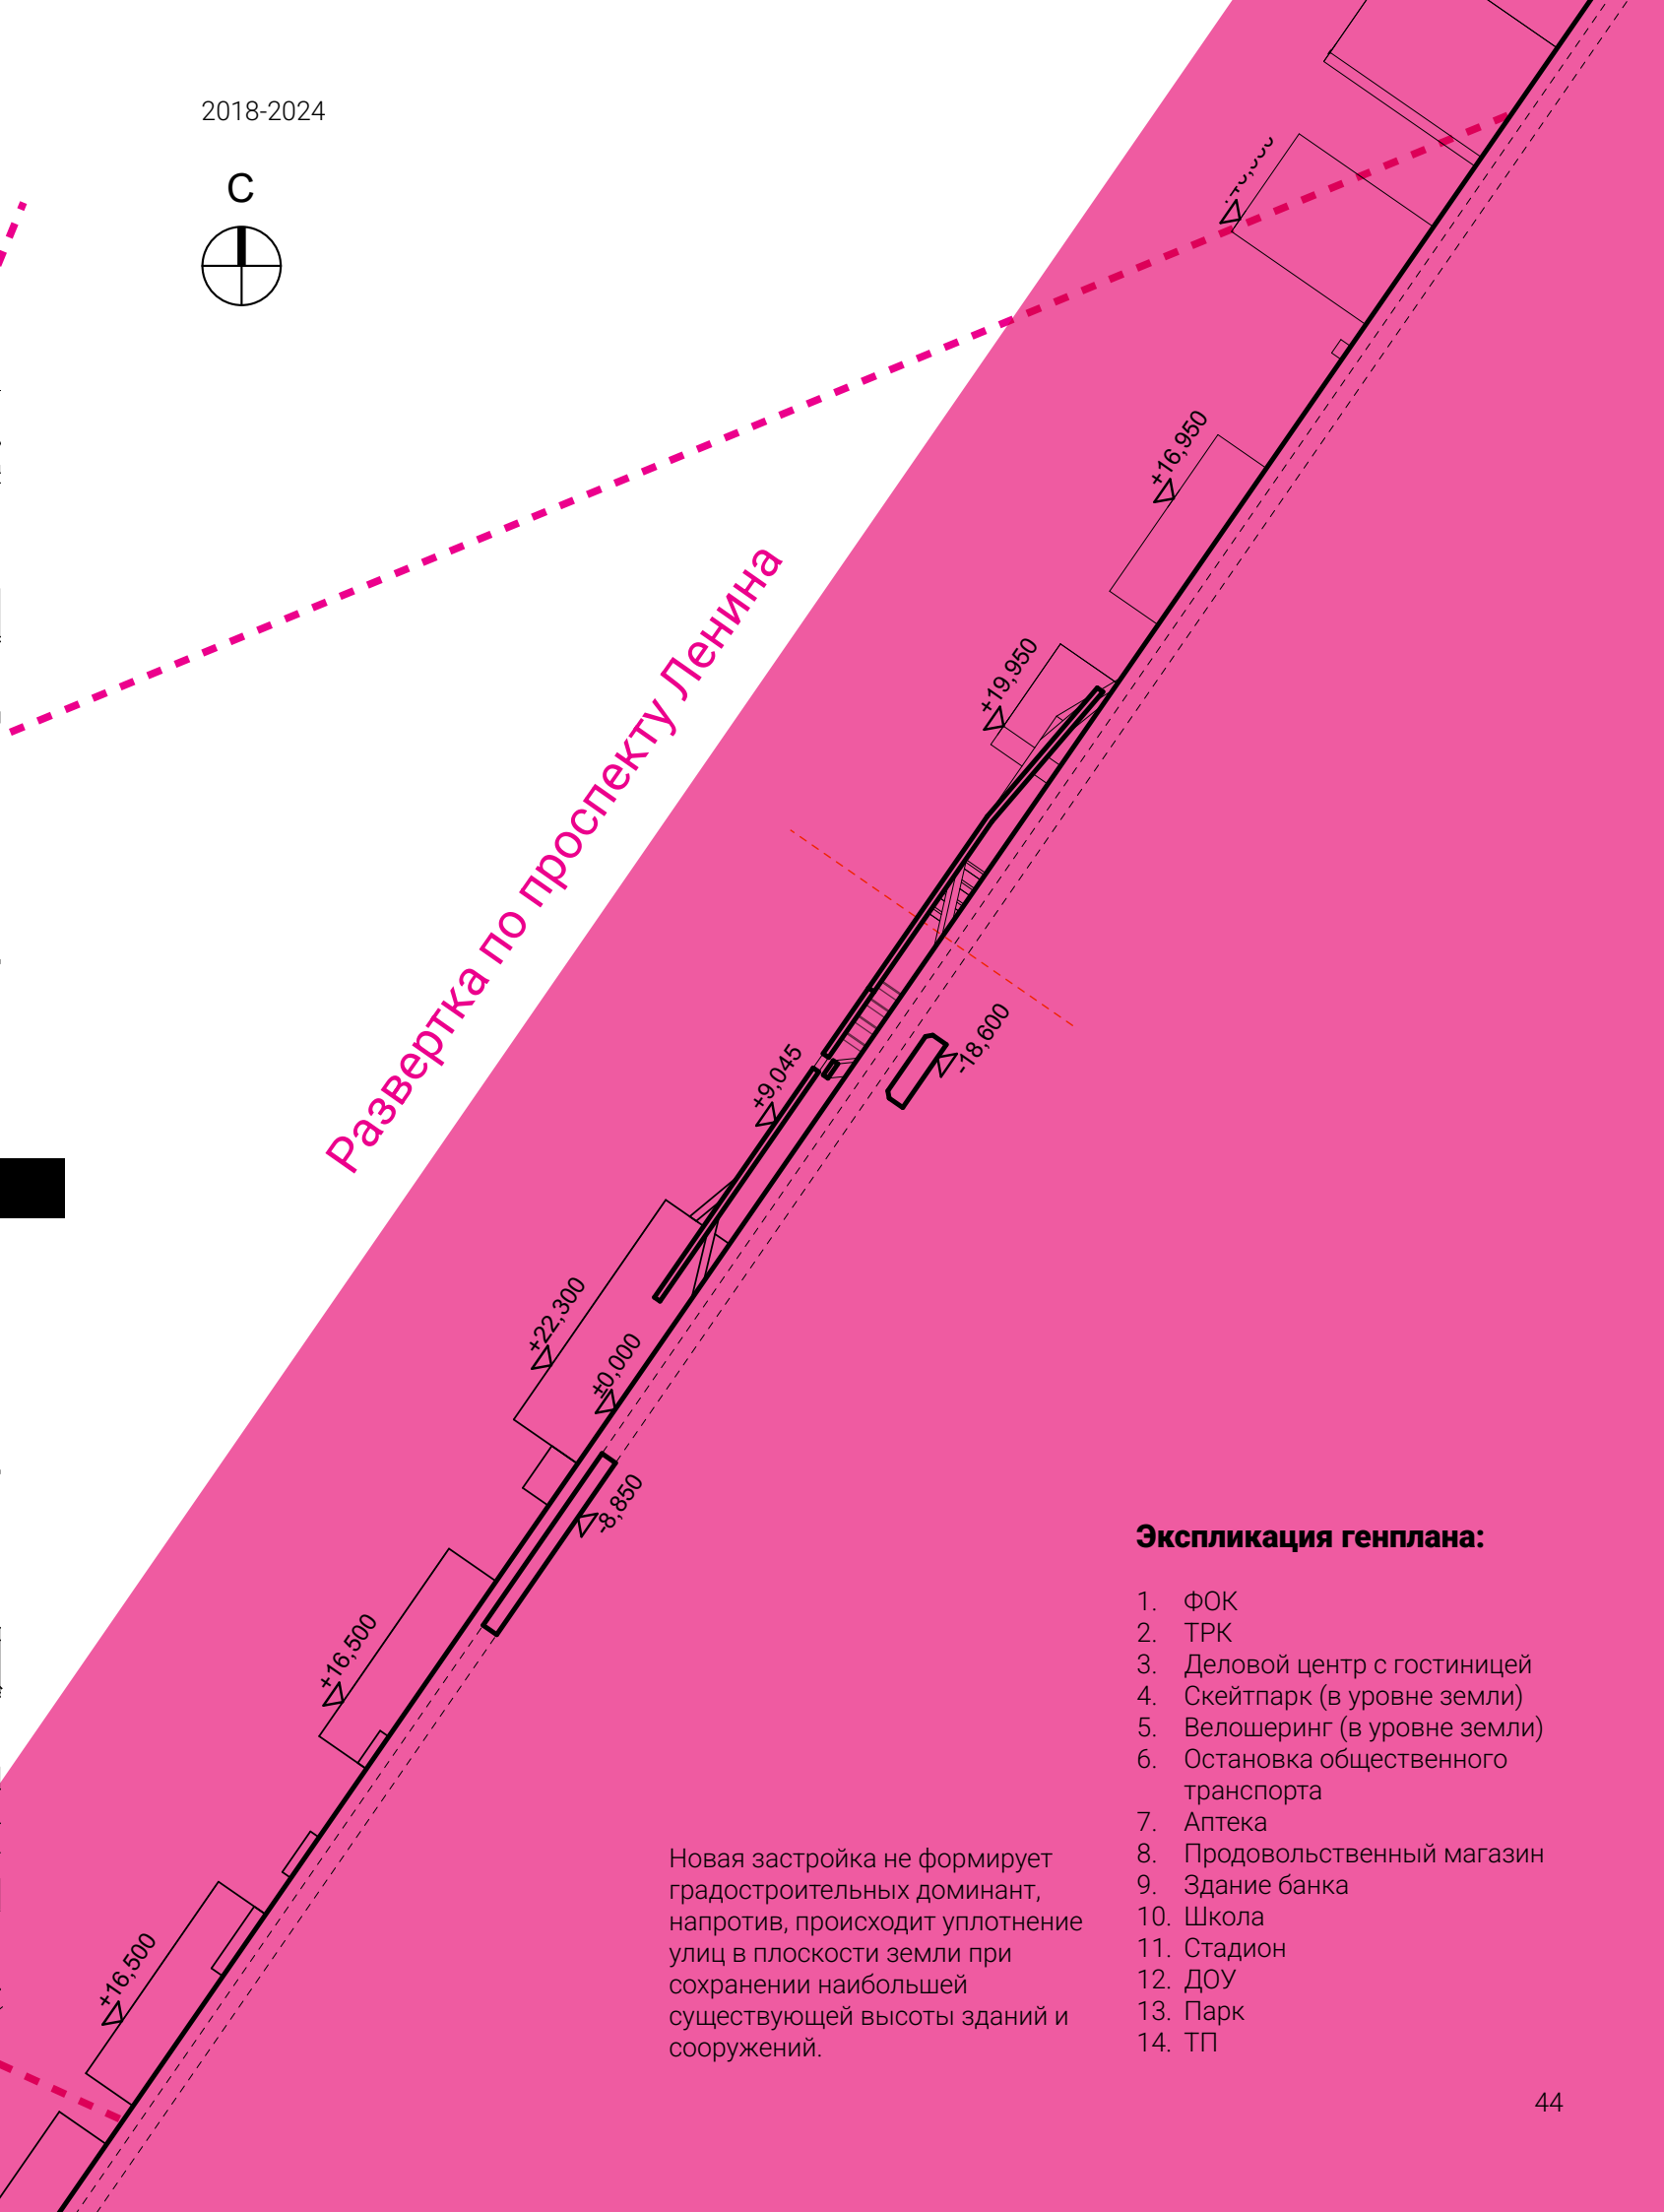


Новая застройка не формирует градостроительных доминант, напротив, происходит уплотнение улиц в плоскости земли при сохранении наибольшей существующей высоты зданий и сооружений.

Экспликация генплана:

- 1. ФОК
- 2. ТРК
- 3. Деловой центр с гостиницей
- 4. Скейтпарк (в уровне земли)
- 5. Велошеринг (в уровне земли)
- 6. Остановка общественного транспорта
- 7. Аптека
- 8. Продовольственный магазин
- 9. Здание банка
- 10. Школа
- 11. Стадион
- 12. ДОУ
- 13. Парк
- 14. ТП

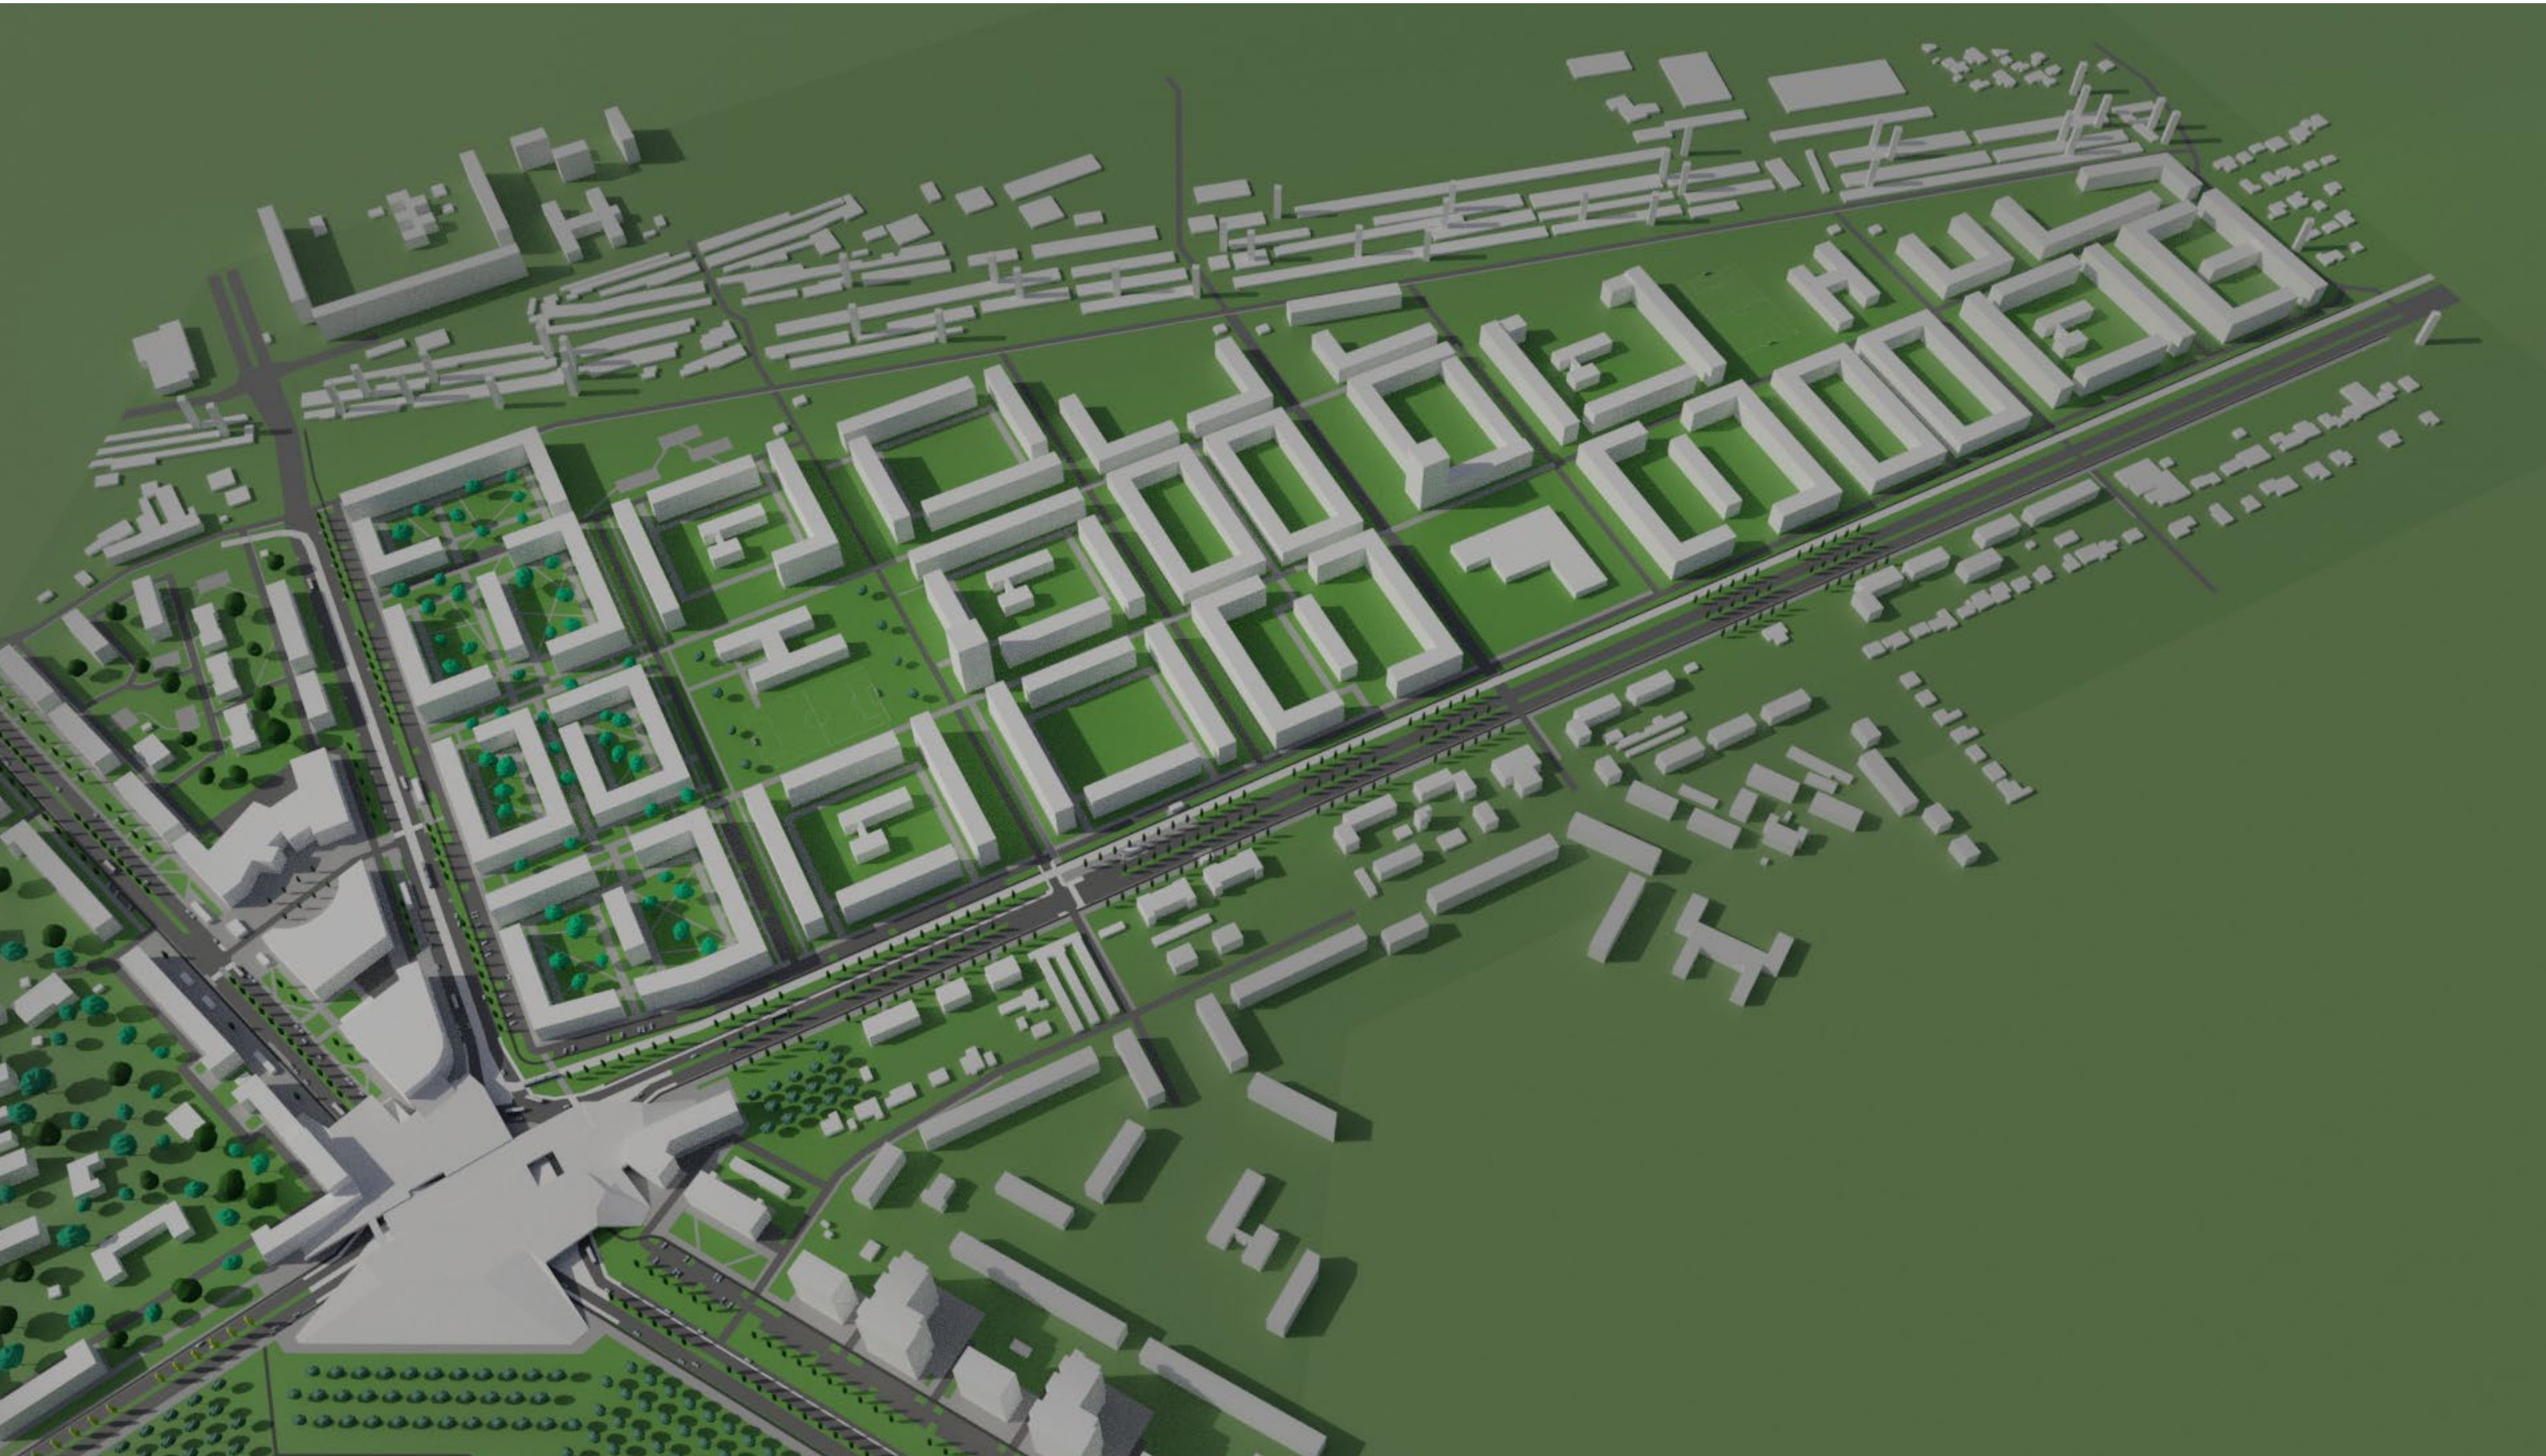



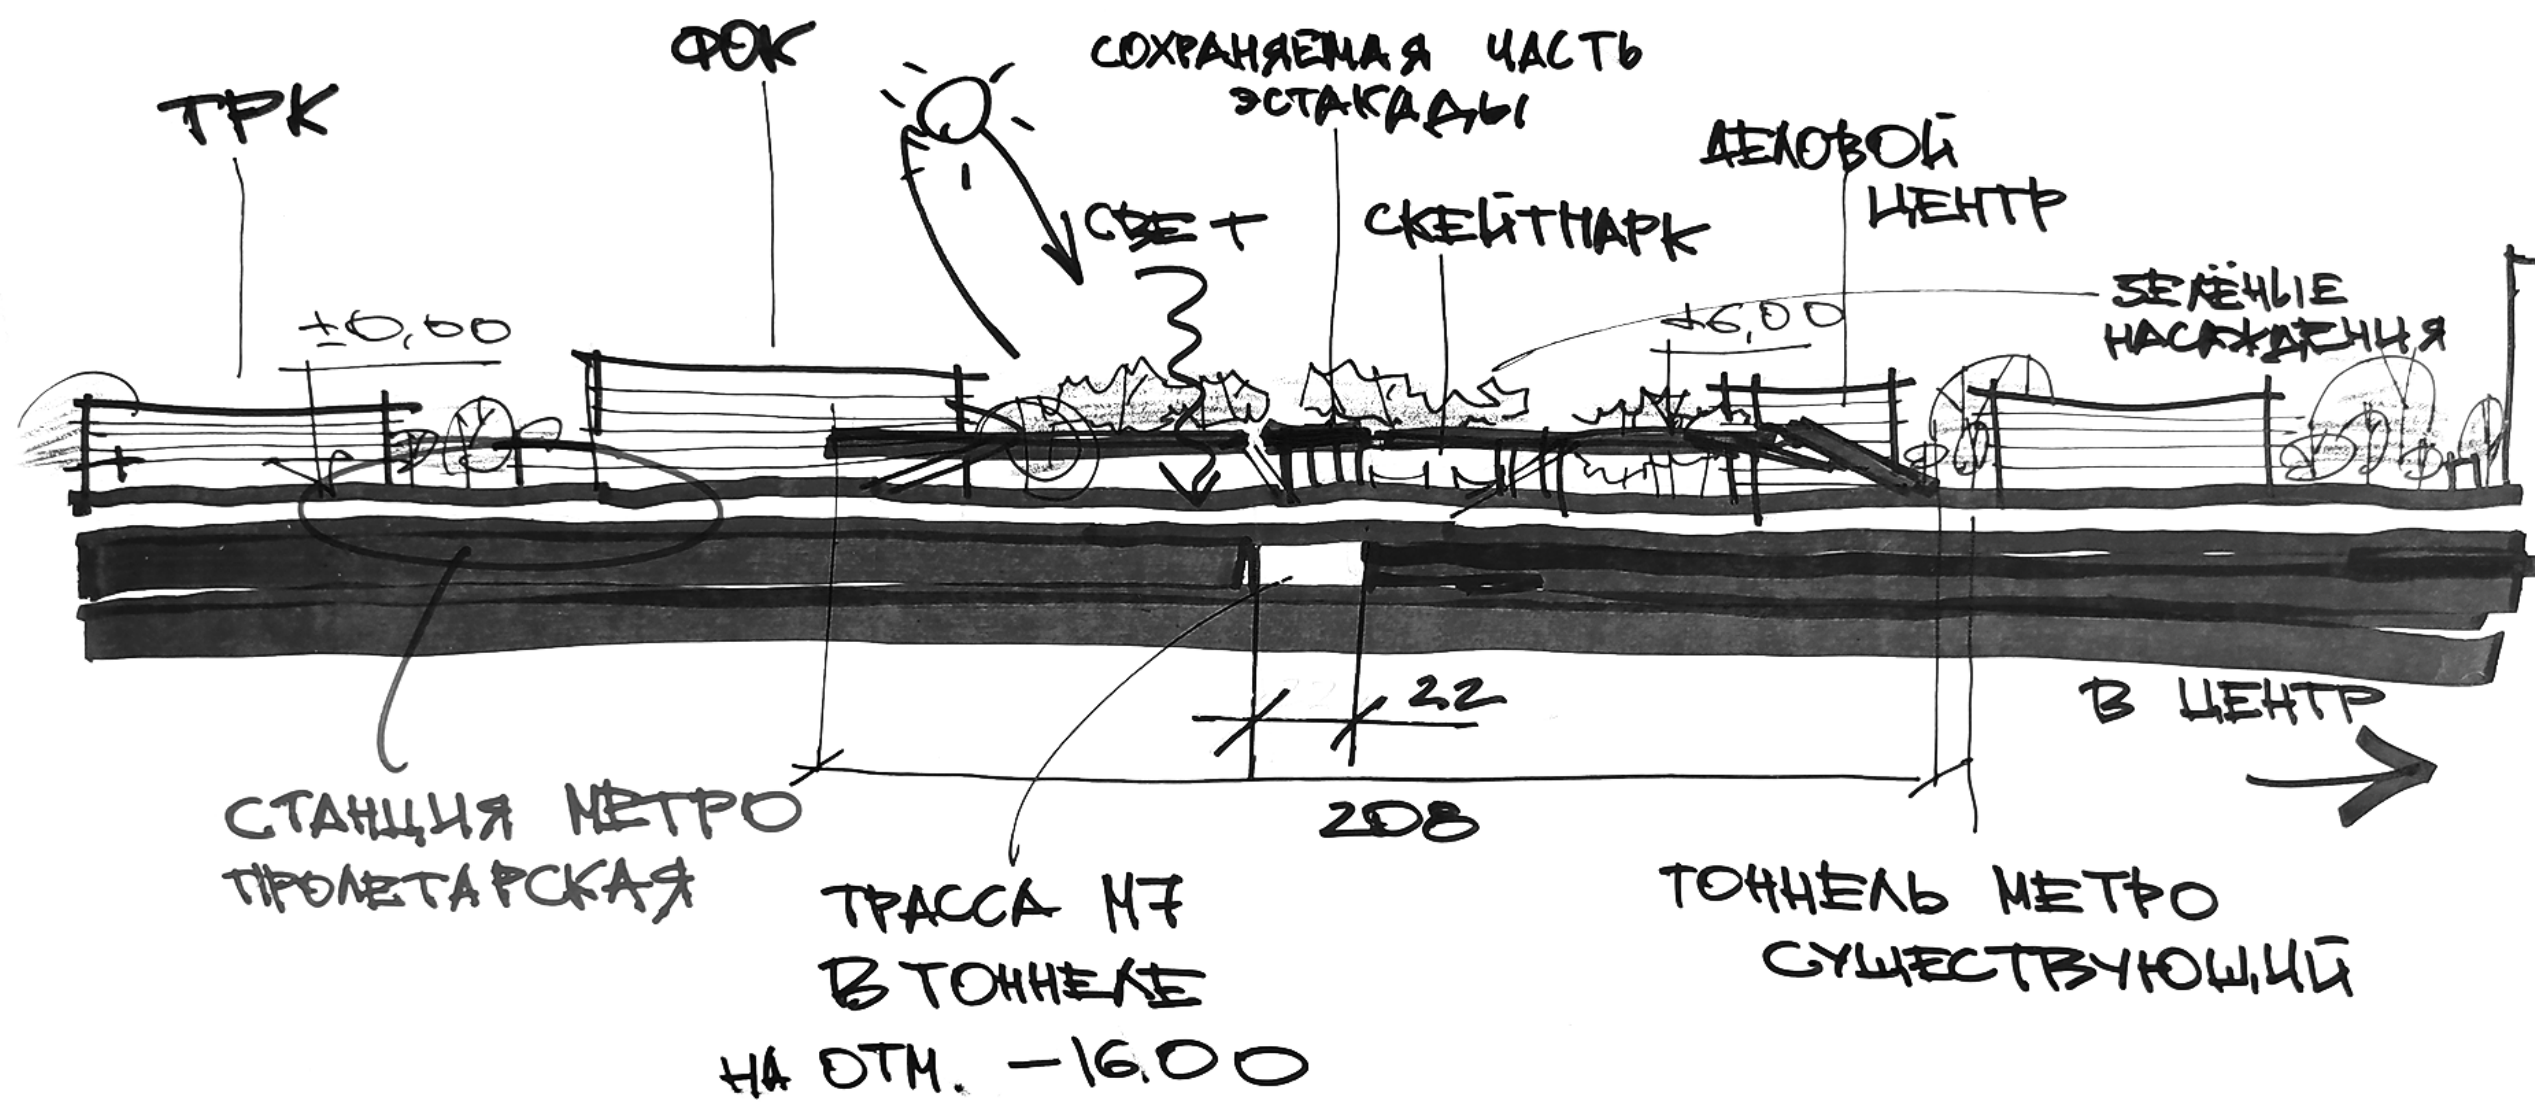



цепь_
советов///

Категория:	Конкурсный проект
Название конкурса:	Открытый Всероссийский конкурс концепций публич-арт объекта «Дом Советов»
Организатор:	Музей «Дом китобоя» (АНО «Музей городской жизни»)
Заказчик:	Администрация г. Калининграда
Год:	2024
Типология:	Малая архитектурная форма
Площадь участка:	144 кв.м
Авторский коллектив:	Александр Мирошин, Александр Гребенников

Авторы предлагают трактовать сохраняемые фасадные панели Дома Советов как звенья цепи. В этом случае предлагаемый объект – символ непрерывности и нерушимости связи времен. Он воплощает в себе образ якоря, фиксирующего определенный этап исторического развития региона.

Технологически такое решение кажется авторам оптимальным – безопасным для лазания по нему, устойчивым статически, устойчивым к вандализму, дешевым в содержании.


Реализация объекта также не представляется авторам сложной или излишне затратной – у каждой из панелей отрезается один из углов, таким образом возможна их вставка друг в друга. Далее после соединения элементов в «цепь» удаленный угол фиксируется в железобетонном монолитном основании. Существующие арматурные сетки панелей соединяются с армированием фундамента.

Для освещения объекта используется LED-подсветка, размещаемая вдоль четвертей оконных блоков. Также возможно устройство наружного освещения всей композиции снизу встроенными в основание светильниками.

Объект предлагается разместить в сквере на месте Кенигсбергского Замка, используя уже сложившуюся геометрию благоустройства, на месте одного из газонов квадратной формы.

Финишное покрытие может быть выполнено из качественной бетонной тротуарной плитки. А в местах примыкания панелей к основанию – производится засыпка декоративным щебнем для ландшафтных работ.

На выбранном участке также возможно размещение скамеек, урн, освещения и других объектов городского благоустройства, по стилистике и материалам поддерживающих общий замысел.

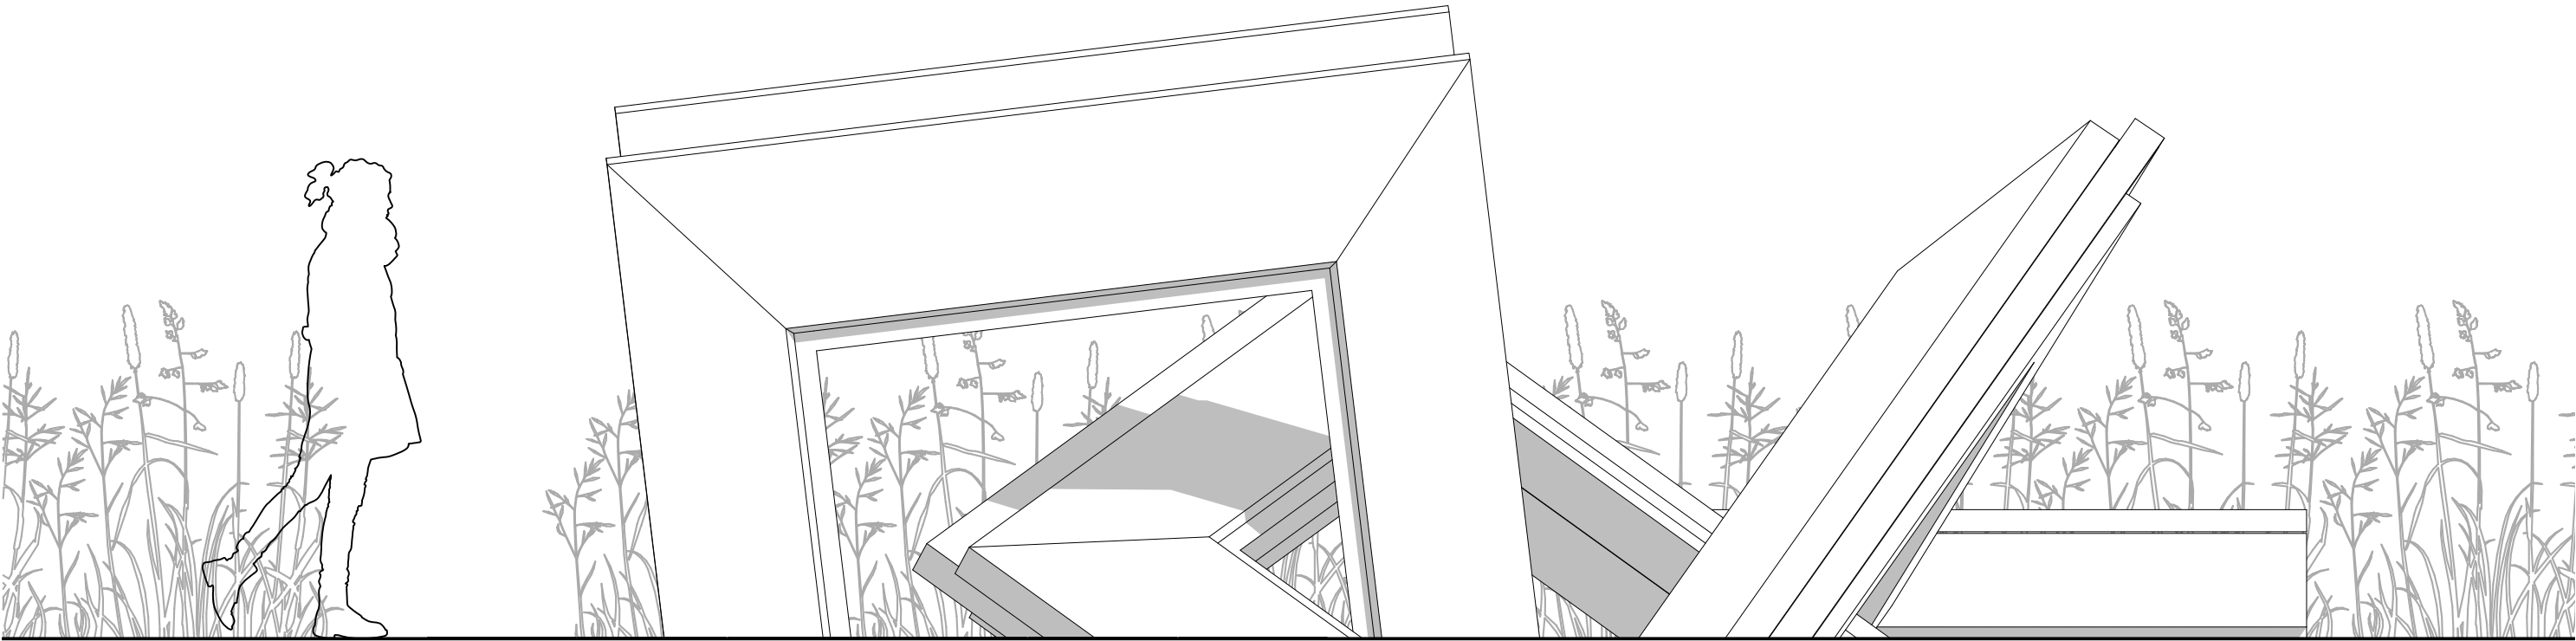


Фасад


1 М



с Генплан 100 М

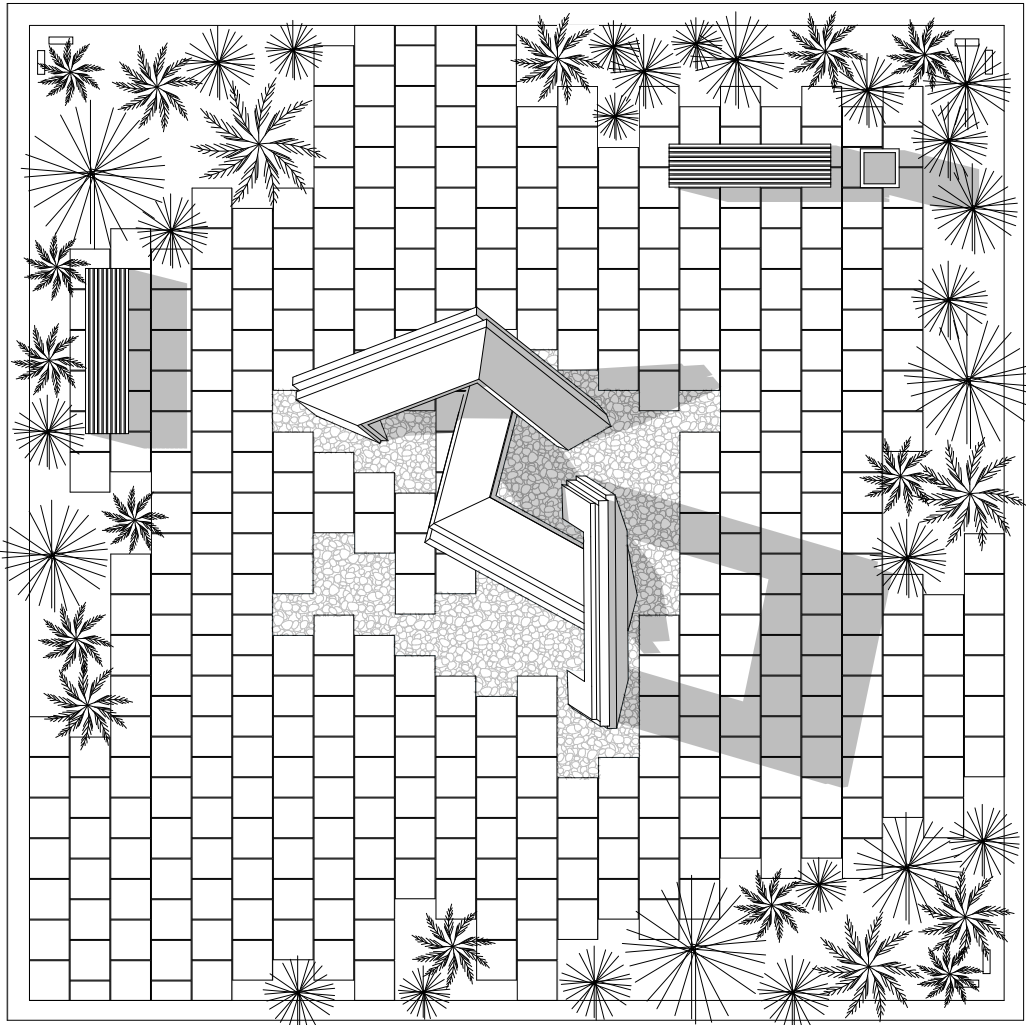

с План 1 М

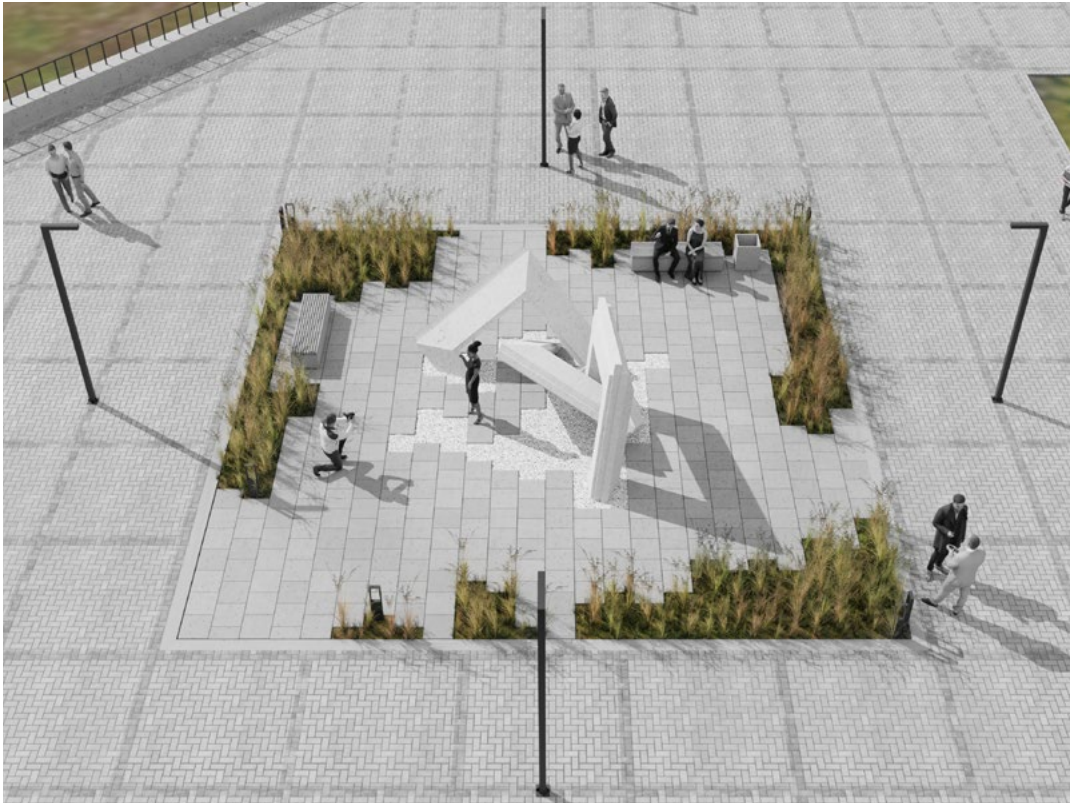



часть_1

/



контакты:

-  Нижний Новгород, Россия
-  +7 (986) 156-78-65 (WhatsApp/Telegram)
-  miroshin.architect@gmail.com
-  a_miroshin